

NEXT STOP

LEMA

ANNO: 2025

Progetto del Master IER per gli **headquarters di Lema** ad Alzate Brianza (MI), per i quali è stato concepito un museo diffuso che racconta l'azienda e che si estende per lo showroom e la zona di produzione.

Il titolo *Next Stop* richiama l'immaginario della **metropolitana**, elemento che ispira e definisce l'intero percorso museale. Ogni tappa diventa una fermata simbolica, un capitolo del **viaggio all'interno dell'universo Lema**, dove valori, storia e vision si intrecciano in un racconto in continua evoluzione.

► APPENDICE



FAI CLICK SUL TASTO PLAY



WAYFINDING

#FFFFFF



#E9E3DE

SOSTEGNI




#9B1C20


FERMATE

METALLO


#000000

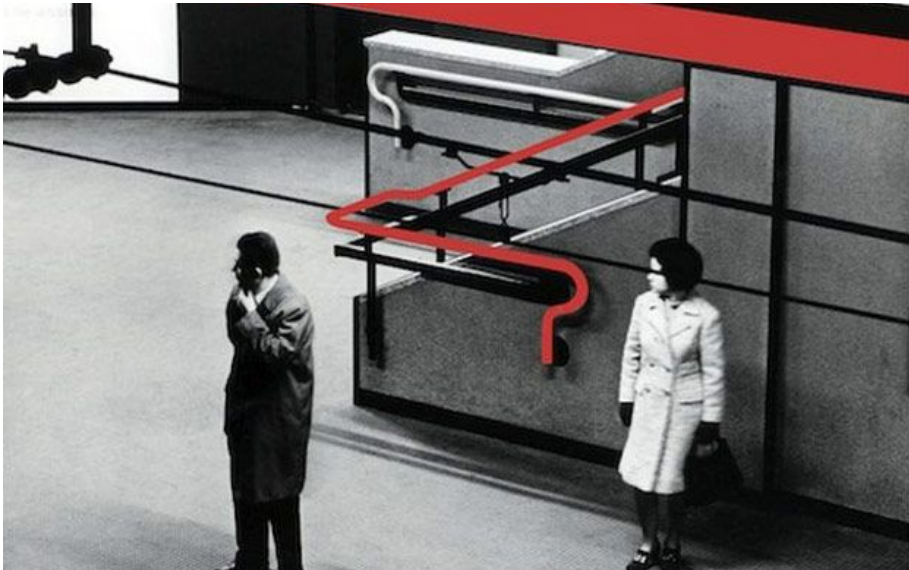


LEIMA

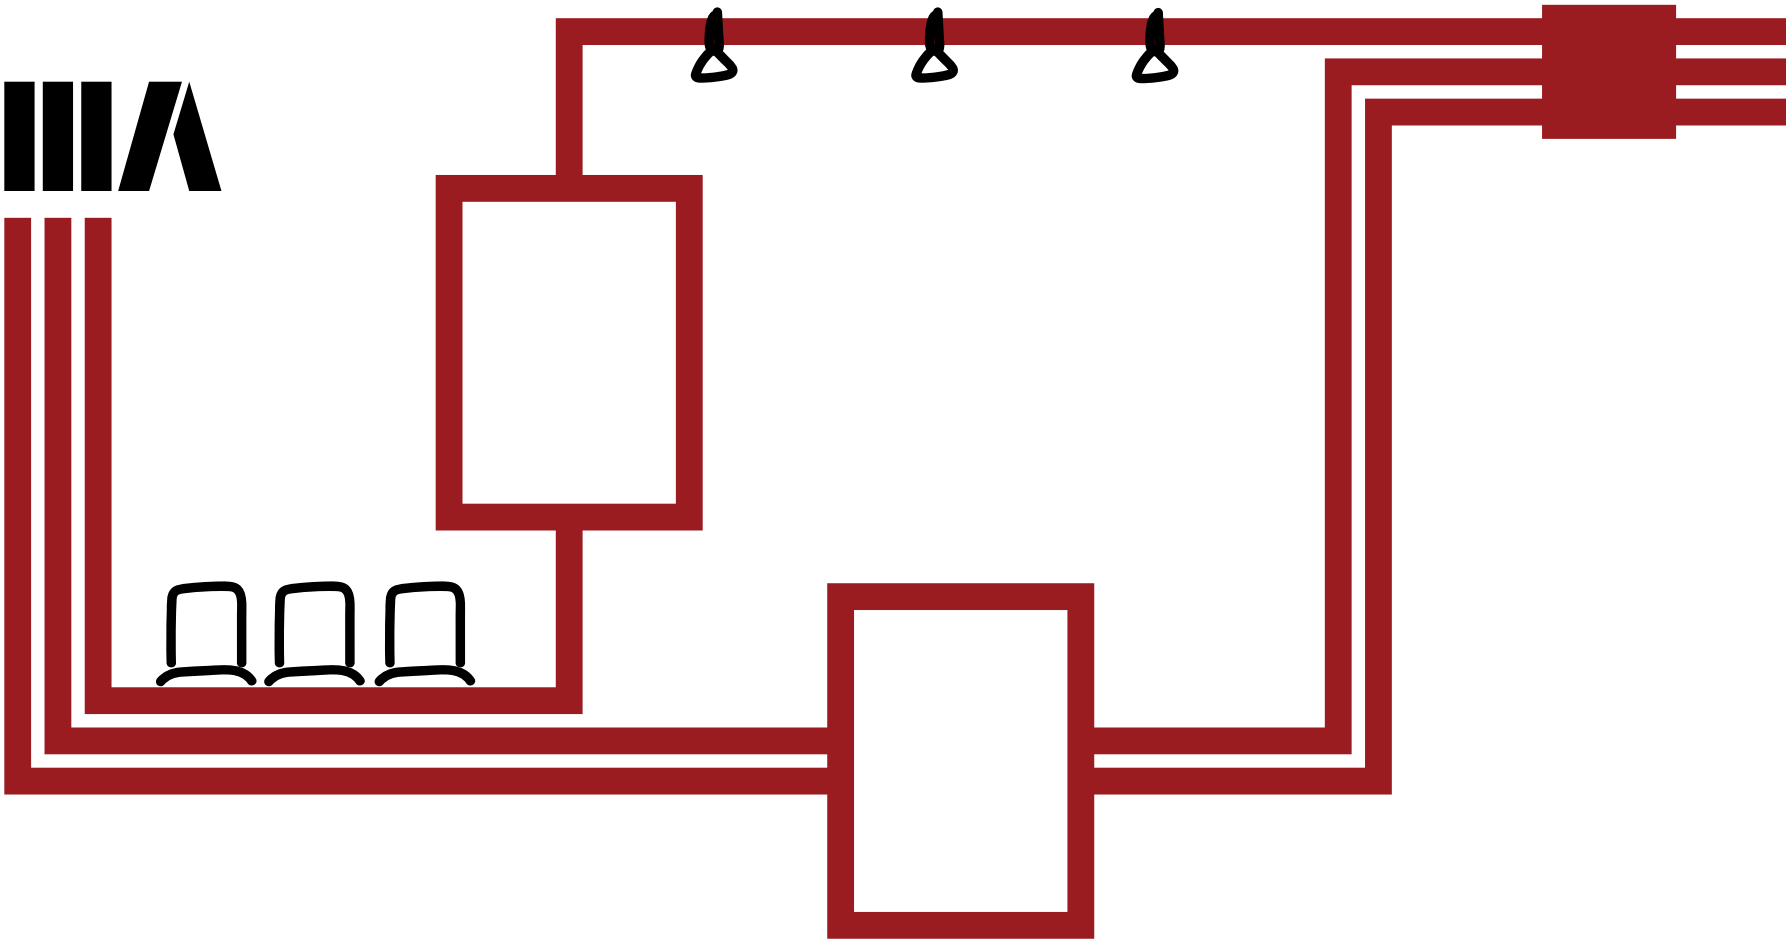


Il percorso si articola in 15 tappe, una all'esterno, dieci nello showroom e quattro nella zona di produzione.

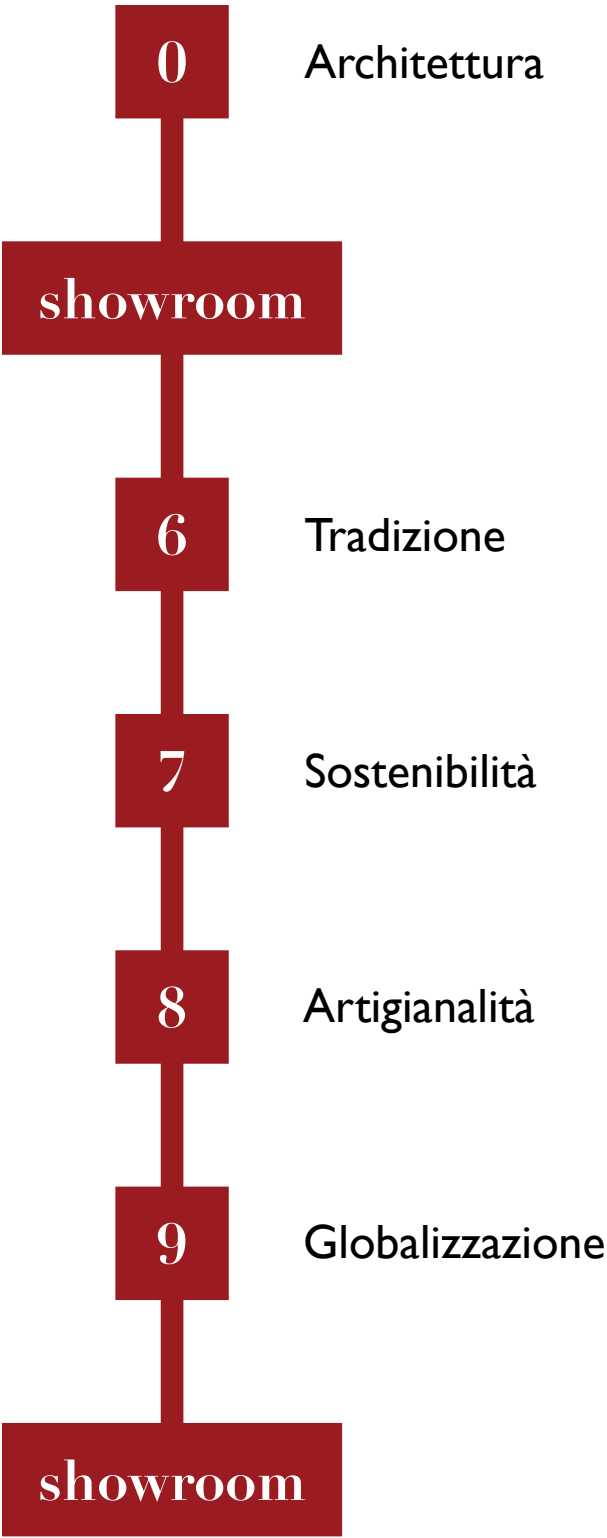

scala 1:1000

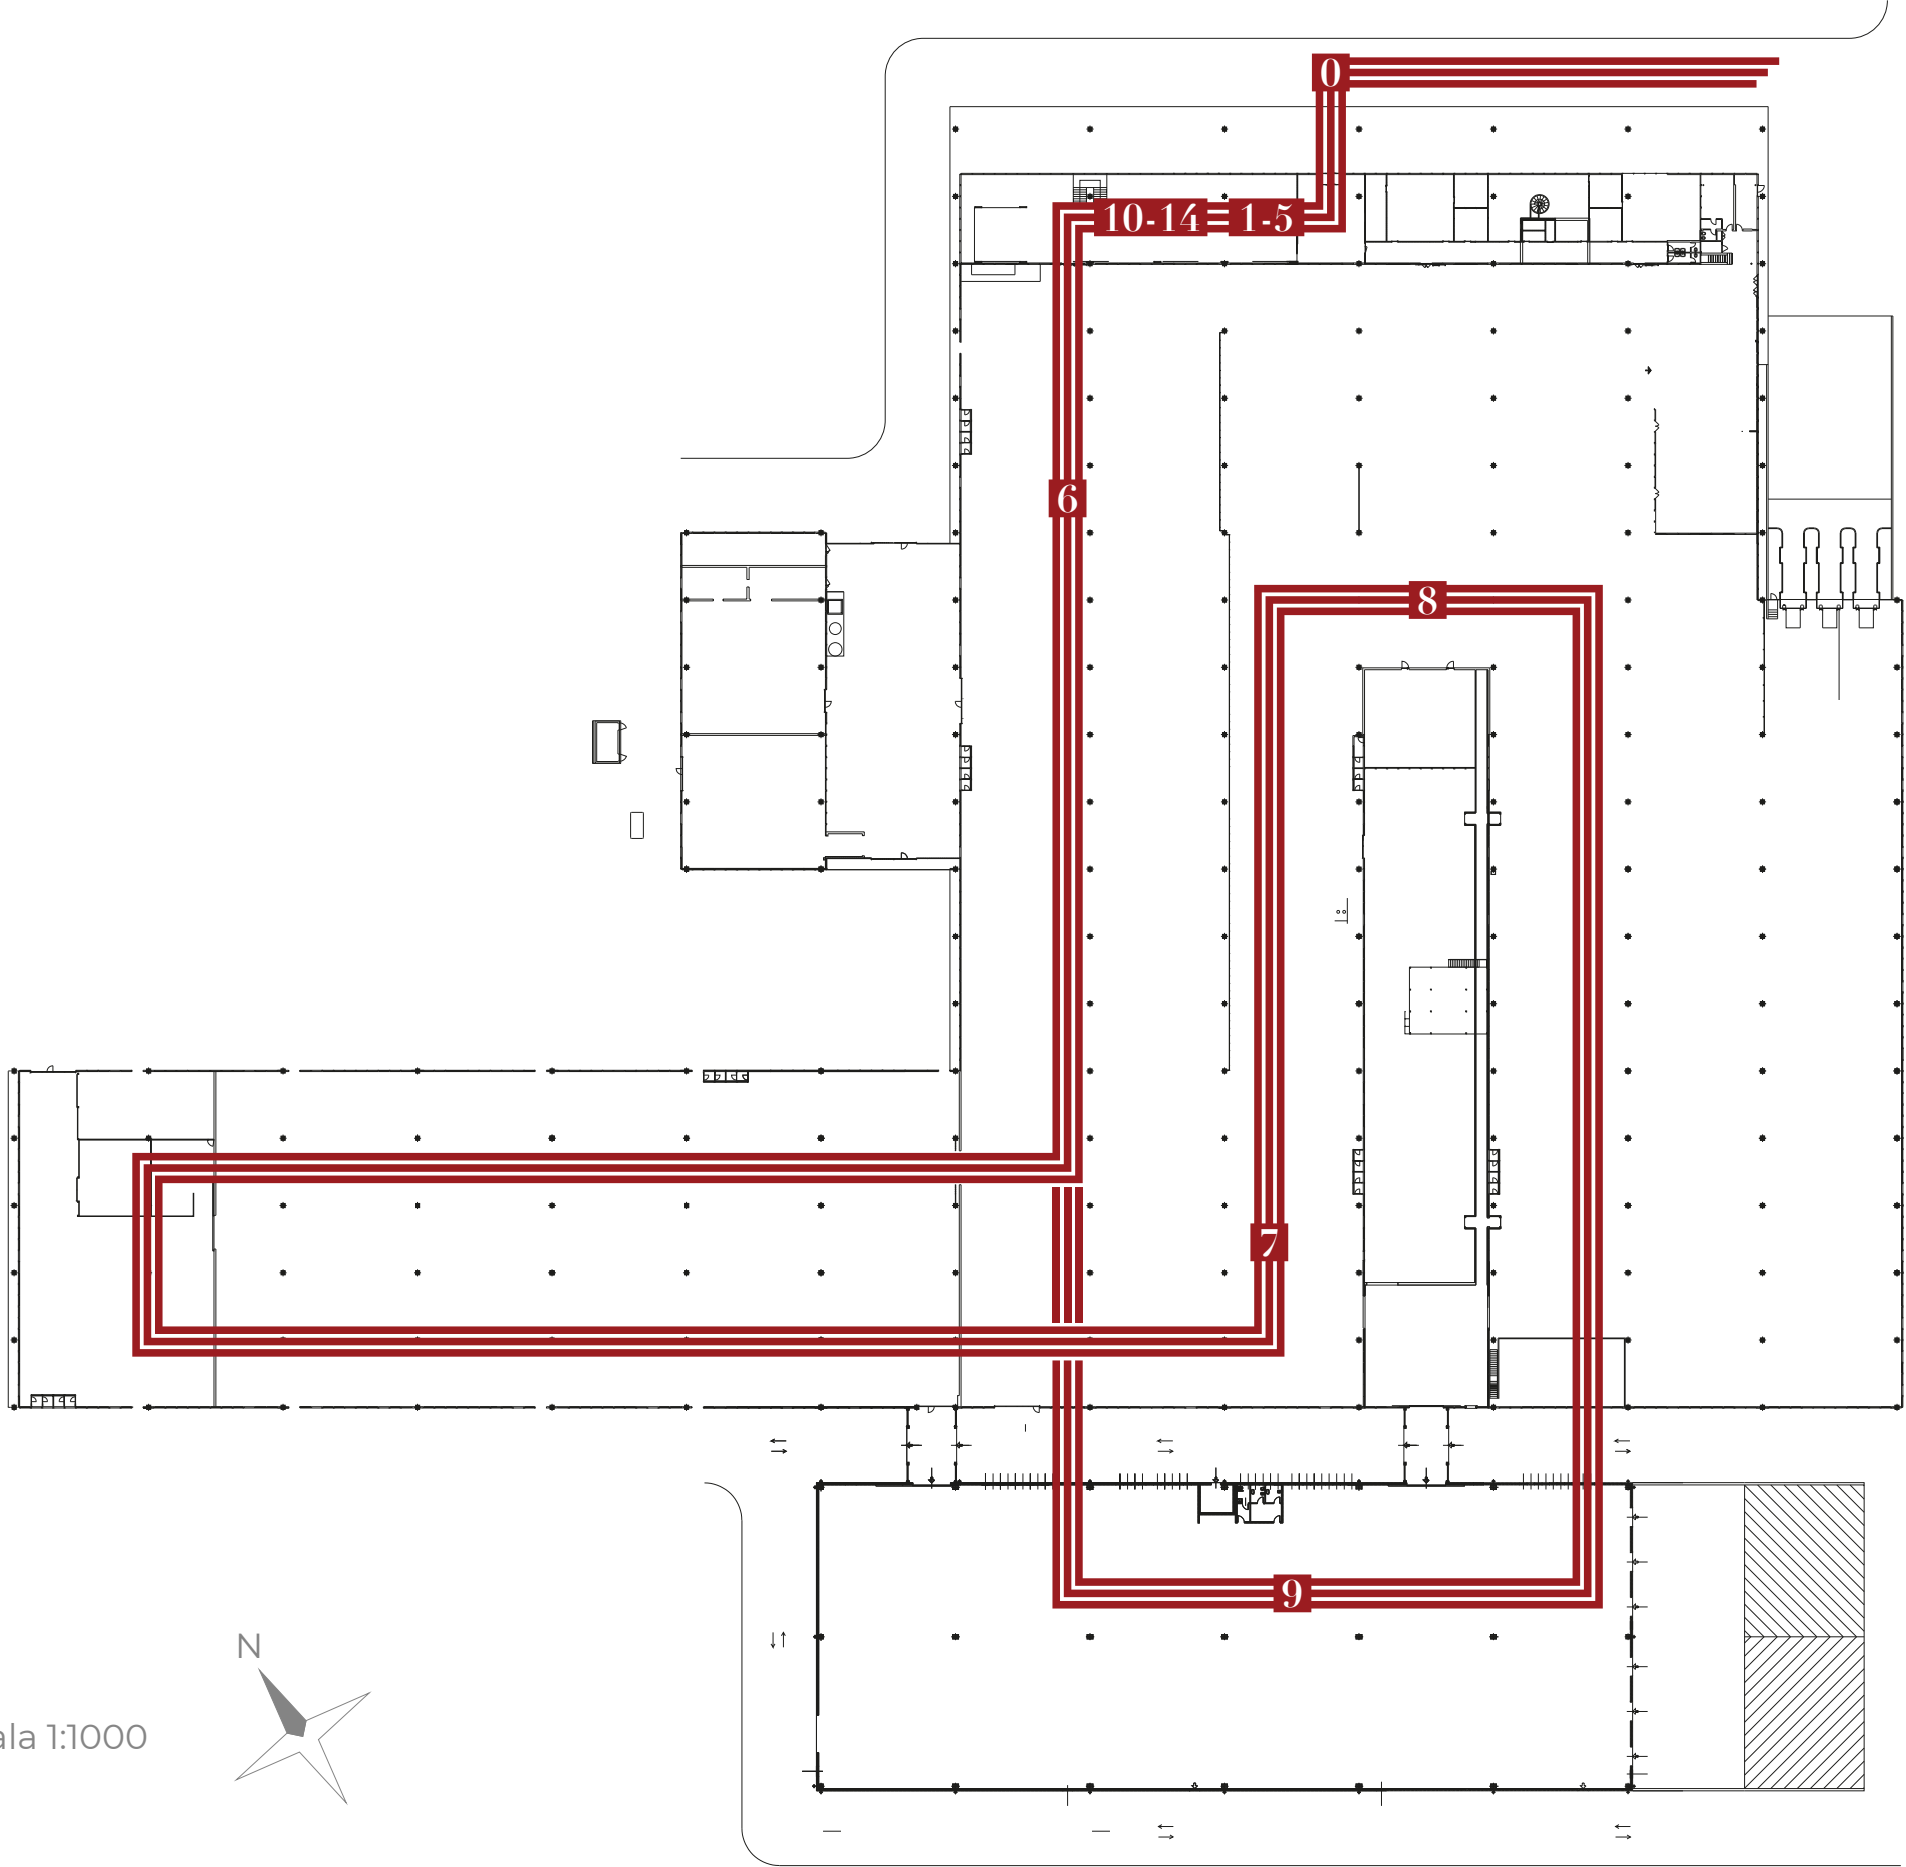


- 1 Passato
- 2 Qualità
- 3 Convivialità
- 4 Eleganza
- 5 Customizzazione

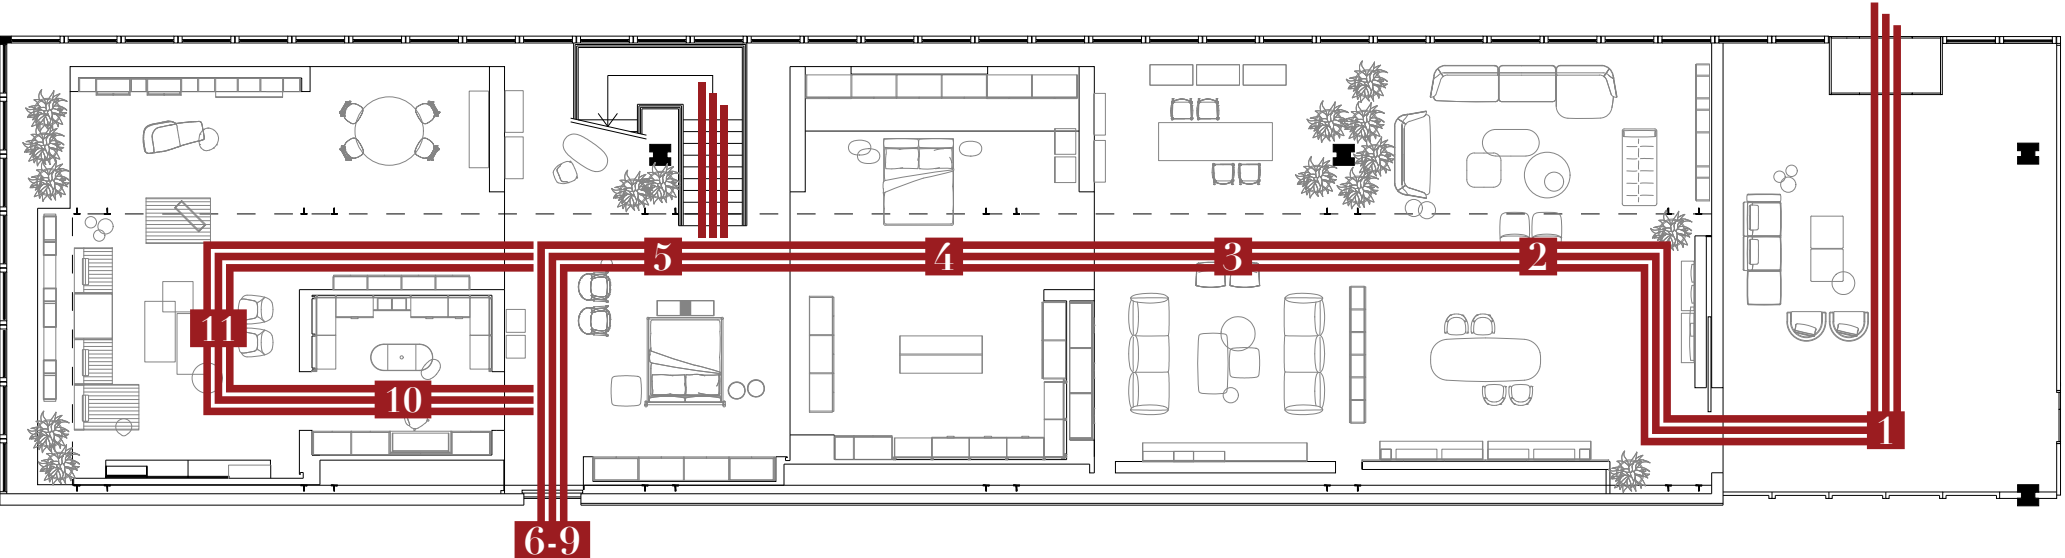

Pianta I livello

- 10 Innovazione
- 11 Relax
- 12 Way of living
- 13 Icons
- 14 Futuro

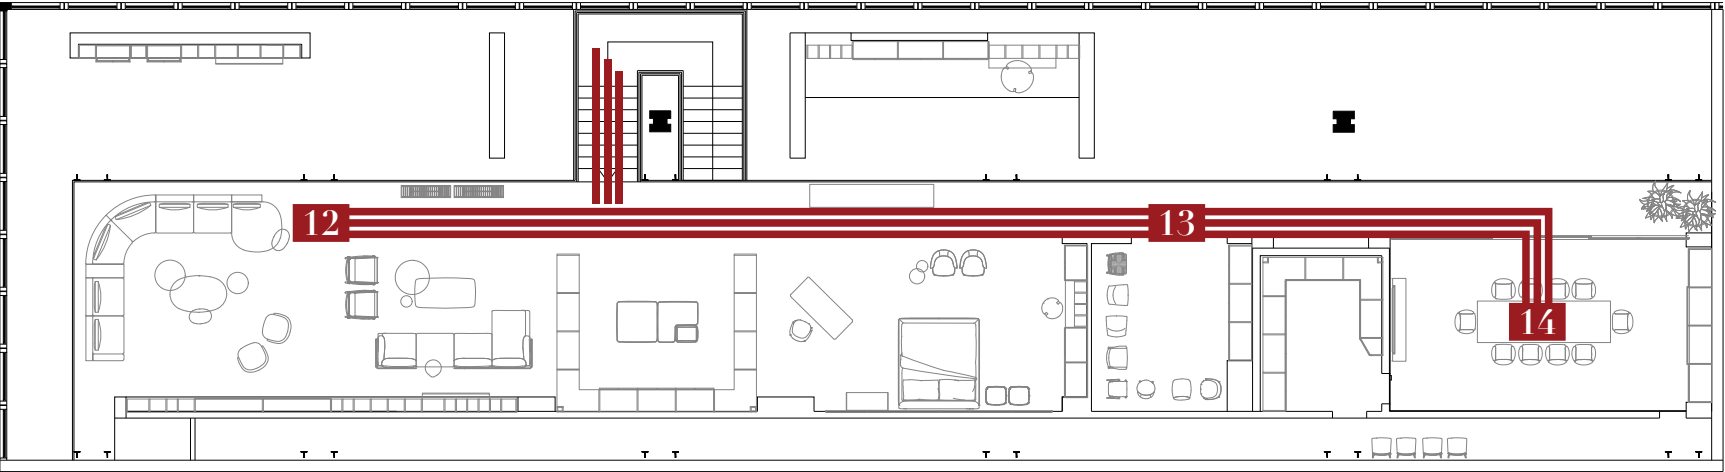

Pianta II livello


scala 1:200



0

Architettura

Il visitatore viene guidato da **tre linee rosse** dipinte sull'asfalto che lo conducono verso una **panca**, la quale lo invita a fermarsi e a leggere un pannello informativo dedicato all'architettura e all'architetto **Angelo Mangiarotti**.

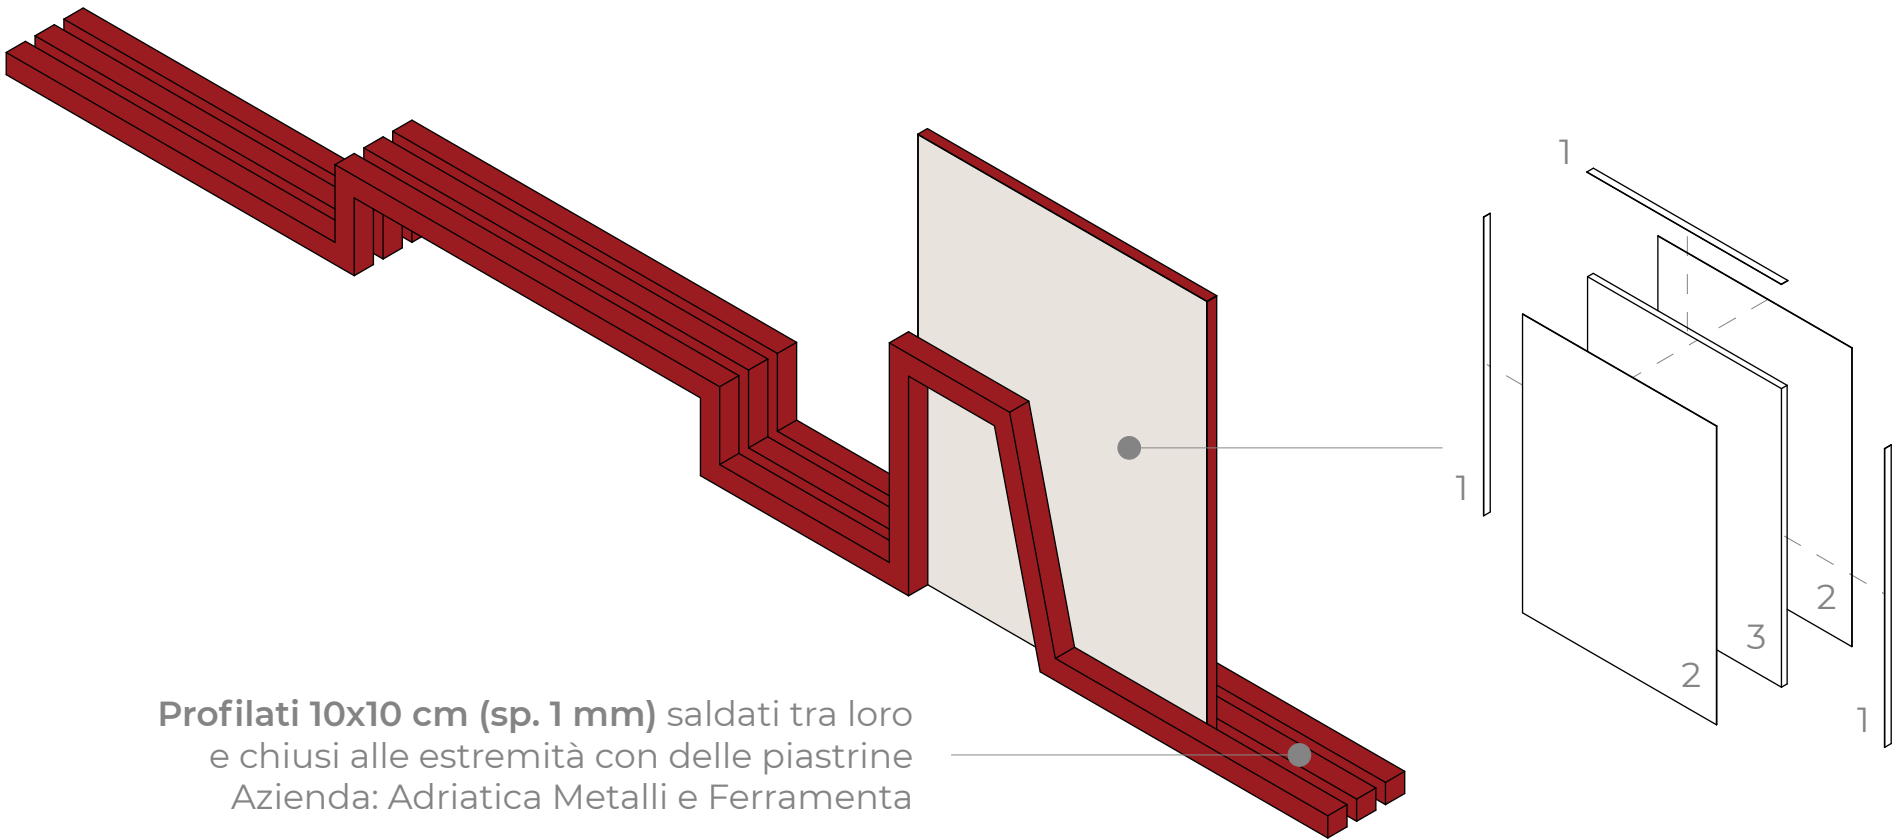

Profilati 10x10 cm (sp. 1 mm) saldati tra loro e chiusi alle estremità con delle piastine
Azienda: Adriatica Metalli e Ferramenta



Grafica a terra

Vernice poliuretanica bicomponente ad alta resistenza
Azienda: CAP Arrenghini

- 1. **Lamiere in alluminio (sp. 2 mm)**
Azienda: Profall
- 2. **Pannello Dibond® digital (sp. 3 mm)**
Azienda: 3A Composites GmbH
- 3. **Distanziale in polistirolo espanso**


Ingresso

Le linee procedono in direzione dell'ingresso dell'edificio, dove un portale richiama l'identità dell'intero percorso.



Logo vetrata

Adesivo in PVC

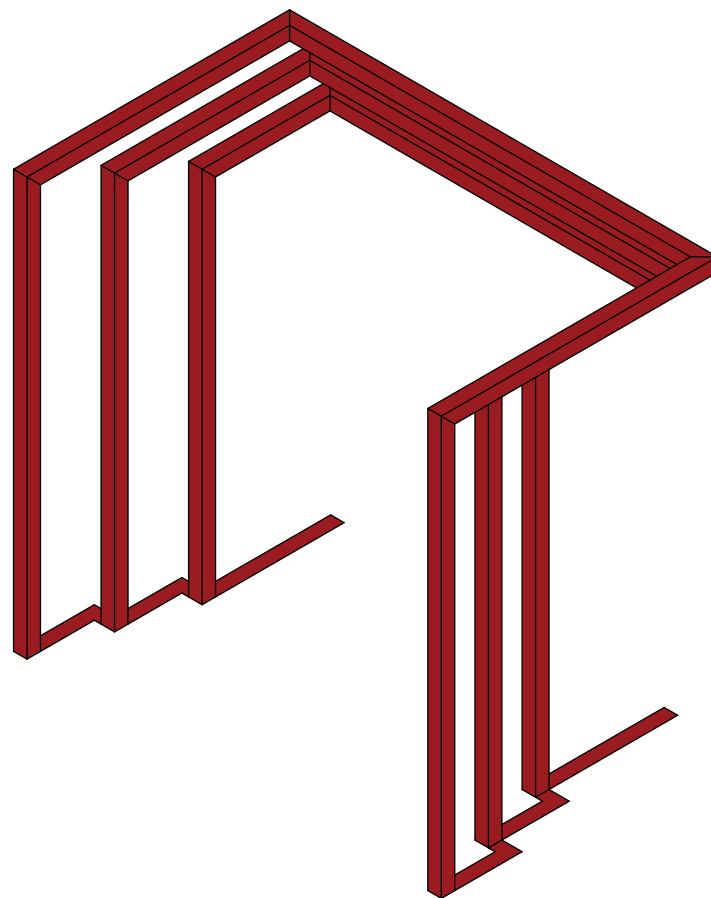

Profilati in alluminio

Azienda: Profall, Adriatica Metalli e Ferramenta

- Resistenza alla corrosione e all'usura
- Rigidità ed elevata resistenza alla trazione
- Leggerezza
- Stabilità dimensionale
- Buone proprietà di sostenibilità ambientale

Analisi CMF

C – Evoca l'identità visiva della metropolitana di Milano e l'eleganza dell'azienda.

M – Rimanda ai sostegni metallici della metro e possiede delle proprietà tecniche indicate per l'allestimento.

F – Rispetta l'allestimento dello showroom.



1

Passato

Nell'atrio il visitatore viene accolto da un video e da una grafica introduttiva: il primo racconta la storia di Lema partendo dal 1930 ad oggi, la seconda indica l'ingresso dello showroom.



Parete laterale

Adesivo in PVC

Vernice acrilica
Azienda: MaxMeyer



Parete frontale

Adesivo in PVC

Vernice per proiezione ARL ad alto contrasto
Screen Goo 2.0 High Contrast 0.85
Azienda: Goo Systems UK



Proiettore Laser 4K
EPSON EH-LS12000
Azienda: Epson



Vernice ARL ad alto contrasto
Azienda: Goo Systems UK


- Aspetto uniforme quando il proiettore è spento
- Non richiede strutture ingombranti
- Più economico di un LED videowall (a parità di dimensioni)

Analisi CMF

C – La vernice grigia, perfetta per ambienti luminosi, consente di aumentare il contrasto delle immagini.

M – È formulata con materiali che riflettono selettivamente la luce del proiettore e che riducono il riflesso della luce ambientale.

F – La finitura opaca non sovrasta visivamente l'allestimento circostante.

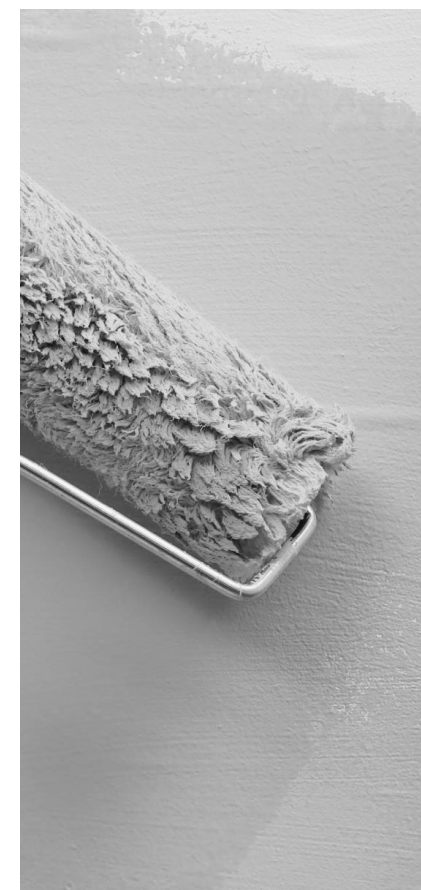

Showroom

L'intero showroom è caratterizzato dalla presenza di guide a soffitto che indicano il percorso da seguire durante la visita.

Cavi per sospensione
ancorati al soffitto

Piastrine a U
per collegamento dei
profilati

Profilato 3,5x3,5 cm
(sp. 2 mm)
Azienda: Profall

Profilato a U
(sp. 2 mm)
Azienda: Profall

Morsetto a C con attacco
per pannelli e area caffè



Apparecchio lineare LED
con binario
incassati nel profilato a U

Bi-magnet linear binario
Azienda: Rimani

Bi-magnet linear 1500
Azienda: Rimani

Flusso luminoso
apparecchio: 1899 lm
TCC: 3000 K
CRI: >90
Potenza: 33 W
Controllo: DALI

Lamiera in alluminio
per chiusura delle estremità
Azienda: Profall

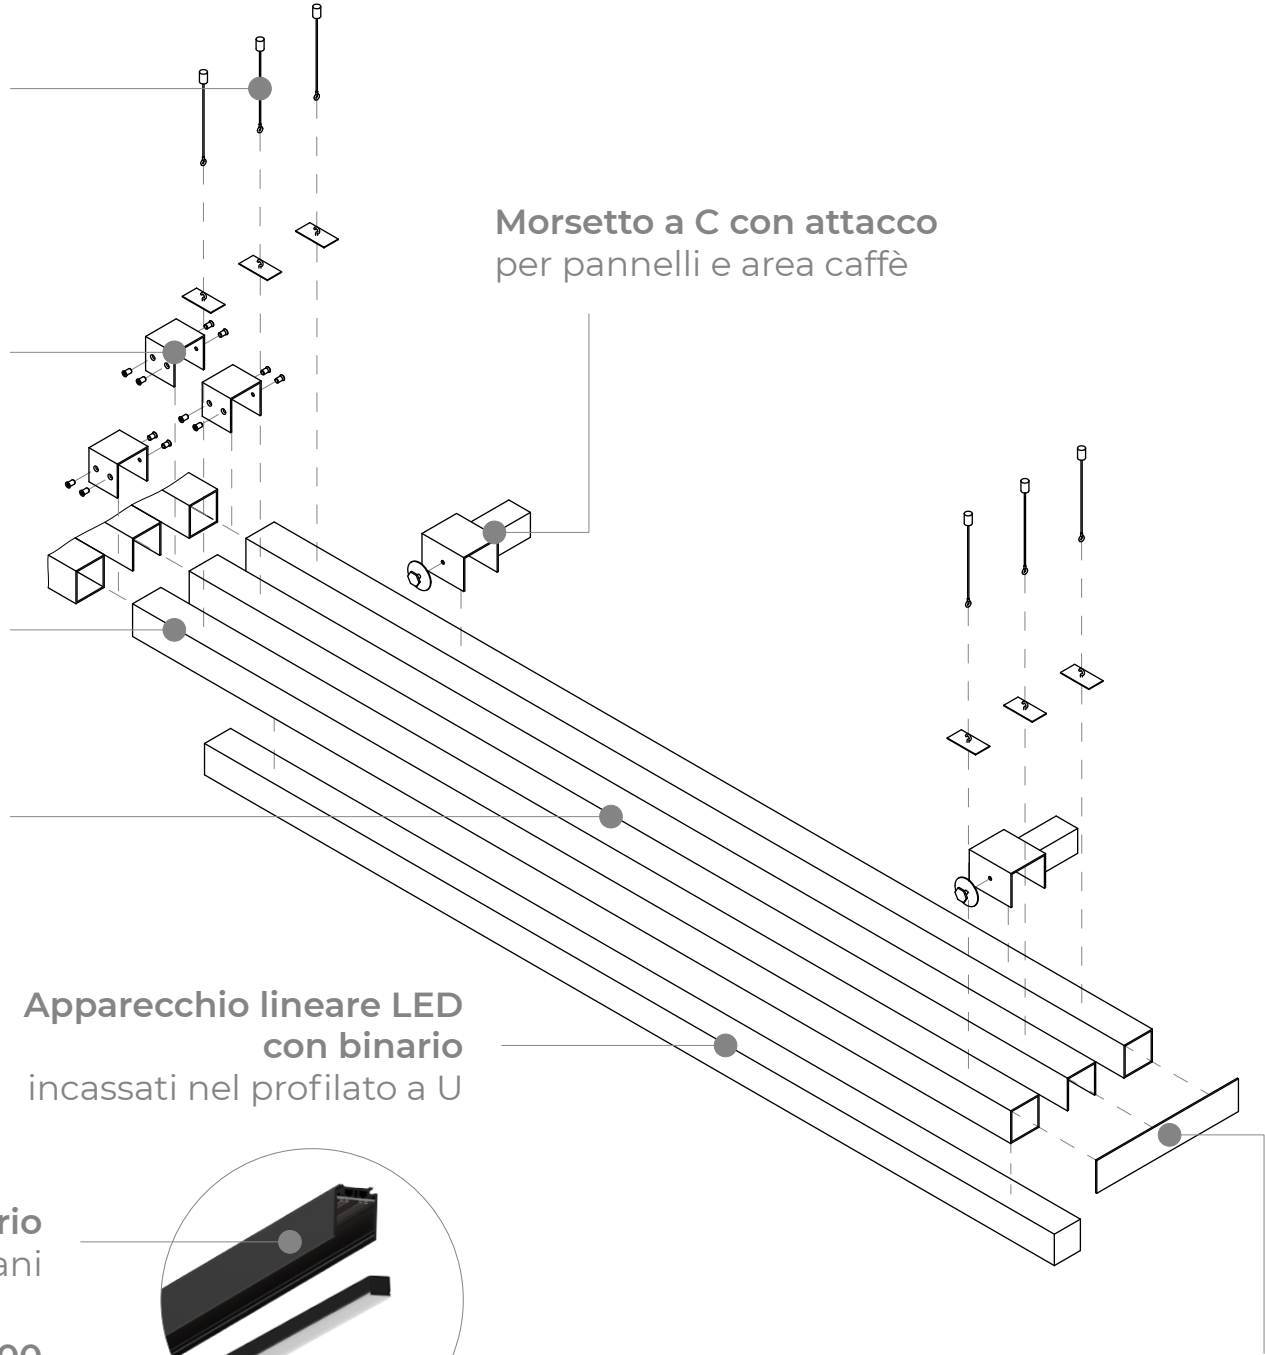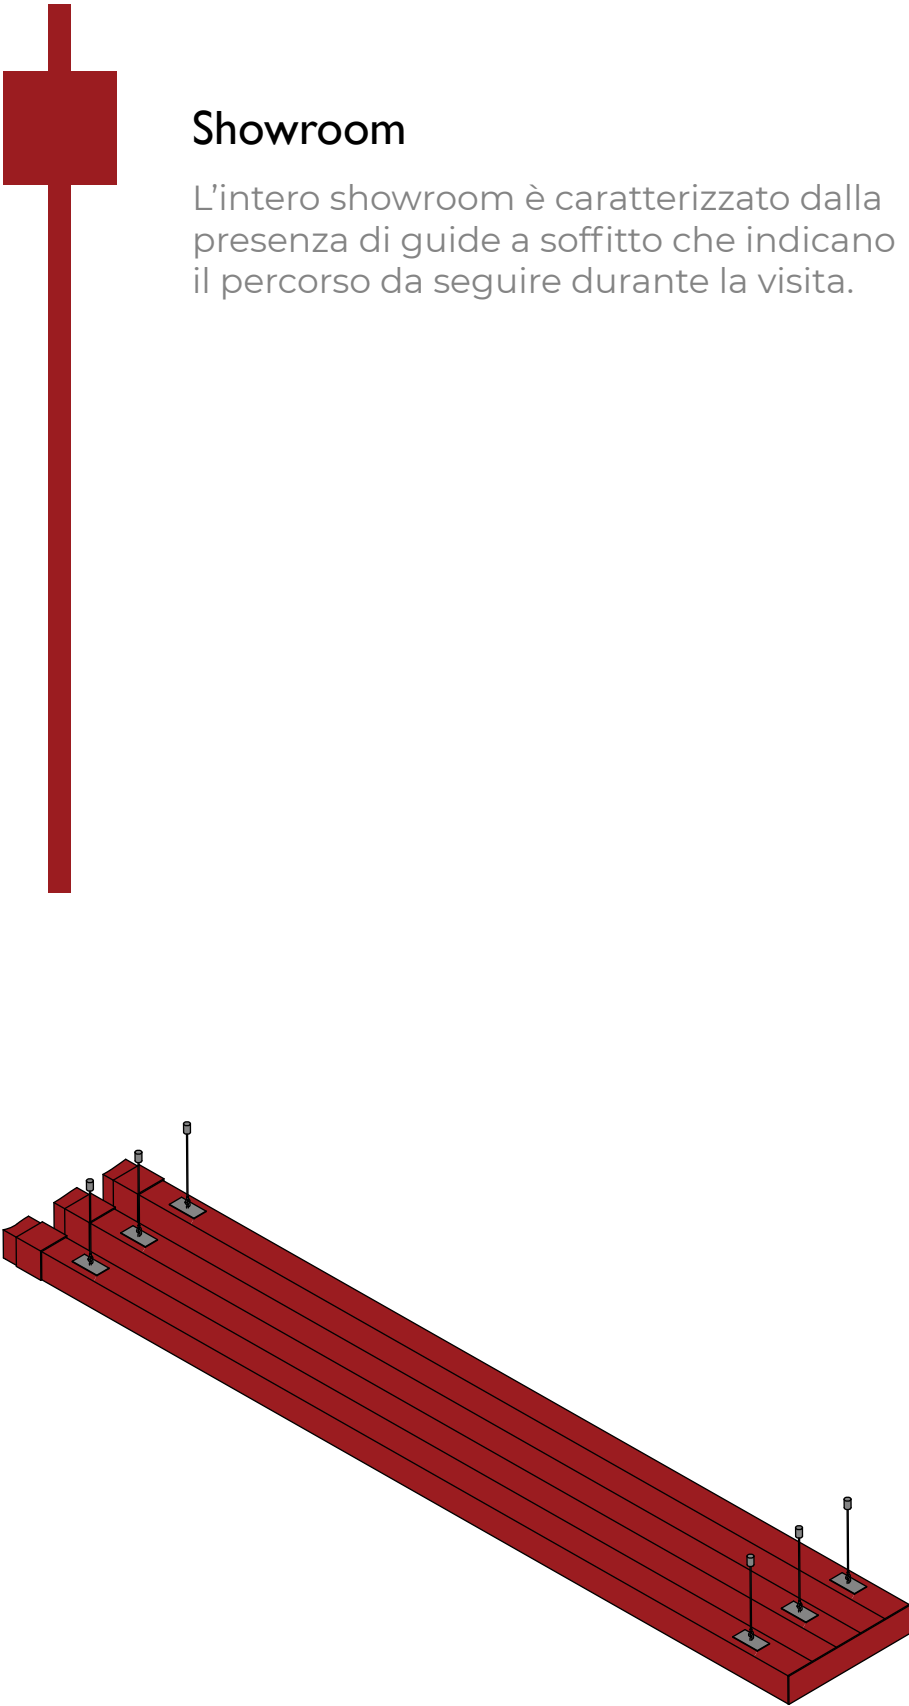


2-5

Qualità, Convivialità, Eleganza, Customizzazione

12

Way of living

Ad ogni fermata all'interno dello showroom il visitatore viene guidato da pannelli esplicativi, ciascuno dedicato a un valore fondamentale di Lema e accompagnato da un tablet che consente di configurare l'arredo esposto, leggere informazioni al riguardo e amplificare l'*experience*, ad esempio controllando le luci spot direzionate su ogni prodotto.

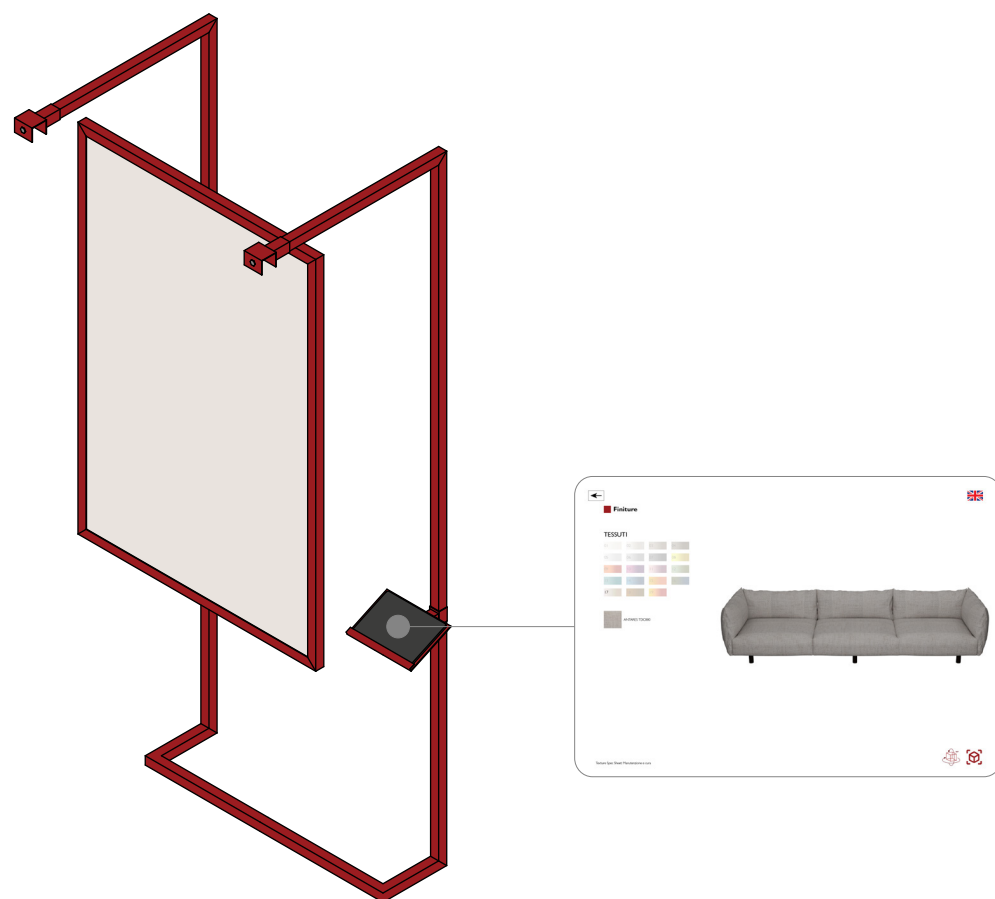

Linotype Didot Std Bold

ABCDEFGHIJKLMNOPQRSTUVWXYZ
abcdefghijklmnopqrstuvwxyz

Gill Sans MT Regular

ABCDEFGHIJKLMNOPQRSTUVWXYZ
abcdefghijklmnopqrstuvwxyz

QUALITÀ

Abbiamo scelto **Qualità** come tappa del nostro viaggio per valorizzare l'eccellenza produttiva di Lema, dove ogni dettaglio riflette cura, maestria artigianale e innovazione. Un impegno costante per creare arredi destinati a durare nel tempo.

We have chosen **Quality** as a stage of our journey to enhance the production excellence of Lema, where every detail reflects care, craftsmanship and innovation. A constant commitment to create furnishings destined to last over time.

inspired
by



craftsmanship

- Orion
- Ast
- Yard Daybed
- Selecta



CONVIVIALITÀ

Abbiamo scelto **Convivialità** come tappa del nostro viaggio per celebrare la capacità di Lema di creare spazi accoglienti e versatili, pensati per favorire l'incontro, la condivisione e il vivere quotidiano con armonia e stile.

We chose **Conviviality** as a stop on our journey to celebrate Lema's ability to create welcoming and versatile spaces, designed to foster connection, sharing, and everyday living with harmony and style.

inspired
by



living together

- Soffio
- Jiku
- Seryasse
- Oydo



WAY OF LIVING

Abbiamo scelto **Way of Living** come tappa del nostro viaggio per esplorare come Lema crei ambienti che vanno oltre il semplice arredo, offrendo soluzioni che riflettono uno stile di vita contemporaneo, personalizzato e in perfetta sintonia con le esigenze di chi li vive.

We chose **Way of Living** as a stop on our journey to explore how Lema creates environments that go beyond mere furniture, offering solutions that reflect a contemporary, personalized lifestyle in perfect harmony with the needs of those who inhabit them.

inspired
by



contemporary
lifestyle

- Venise
- Selecta
- Booken



Dibond® digital

Azienda: 3A Composites GmbH

- Per applicazioni in ambienti interni ed esterni
- Rigidità e robustezza
- Leggerezza
- Resistenza ai raggi UV
- Risultati di stampa precisi e ad alta definizione

Analisi CMF

C – Il bianco, unico colore disponibile per questo prodotto, ben si presta alla stampa digitale.

M – Coerente con il resto dell'allestimento e proprietà tecniche indicate per la sua applicazione.

F – La finitura opaca garantisce una buona leggibilità dei testi, evitando di comprometterla a causa dei riflessi di luce.

6-9

Tradizione, Sostenibilità, Artigianalità, Globalizzazione

Al visitatore vengono fornite cuffie con cancellazione del suono per entrare in produzione, dove grafiche a terra tracciano il percorso da seguire, sempre accompagnato da una guida.



Grafica a
pavimento zona
produzione

Vernice poliuretanica
bicomponente ad alta
resistenza
Azienda: CAP Arrenghini

7 **Sostenibilità**

Il design che rispetta il domani — 

Grafica a parete
ingresso
produzione

Vernice acrilica
Azienda: MaxMeyer



10

Innovazione

14

Futuro

Il visitatore può interagire con **monitor touch screen** per esplorare i contenuti multimediali relativi alle nuove tecnologie, i materiali sperimentali e le prospettive future adottate dall'azienda, sostituendo i pannelli e i tablet presenti nelle altre fermate dello showroom.


13

Icons

Una grafica stampata introduce il visitatore alla scoperta della sezione dedicata ai prodotti iconici dell'azienda.



Schermi touch

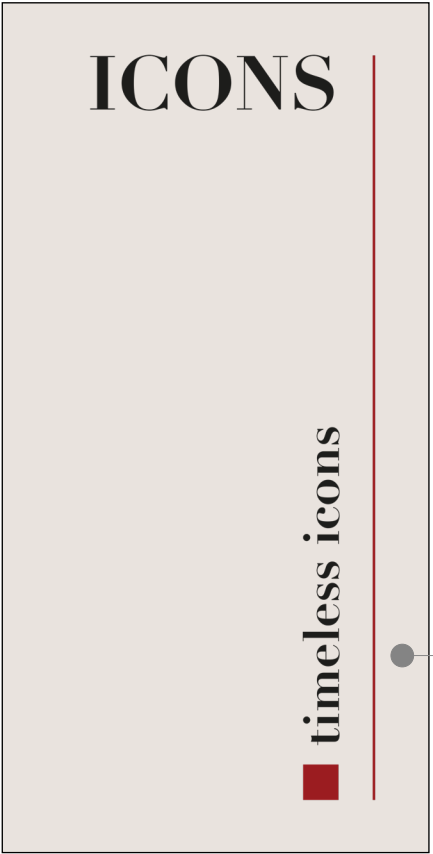


Adesivo in PVC

11

Relax


Prima di concludere il percorso al secondo livello dello showroom, il visitatore potrà accomodarsi sui divani e godersi un caffè.



Il **mobile bar** è stato progettato integrando il concept al sistema modulare Plain di Lema.

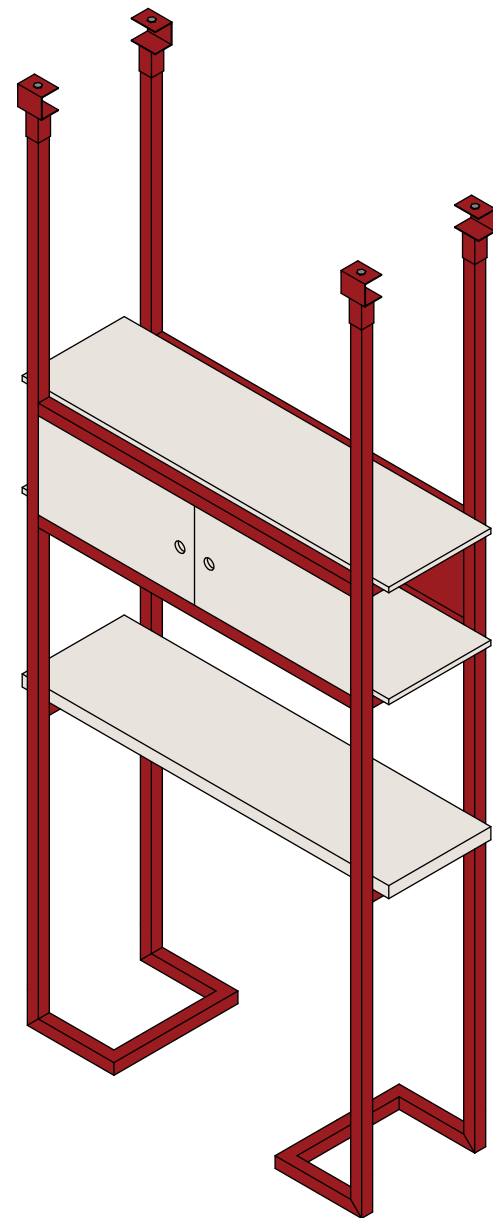


Prenditi una pausa,
assapora il momento ■



Un esploso assonometrico mostra la disposizione degli elementi allestitivi nello showroom e all'esterno.

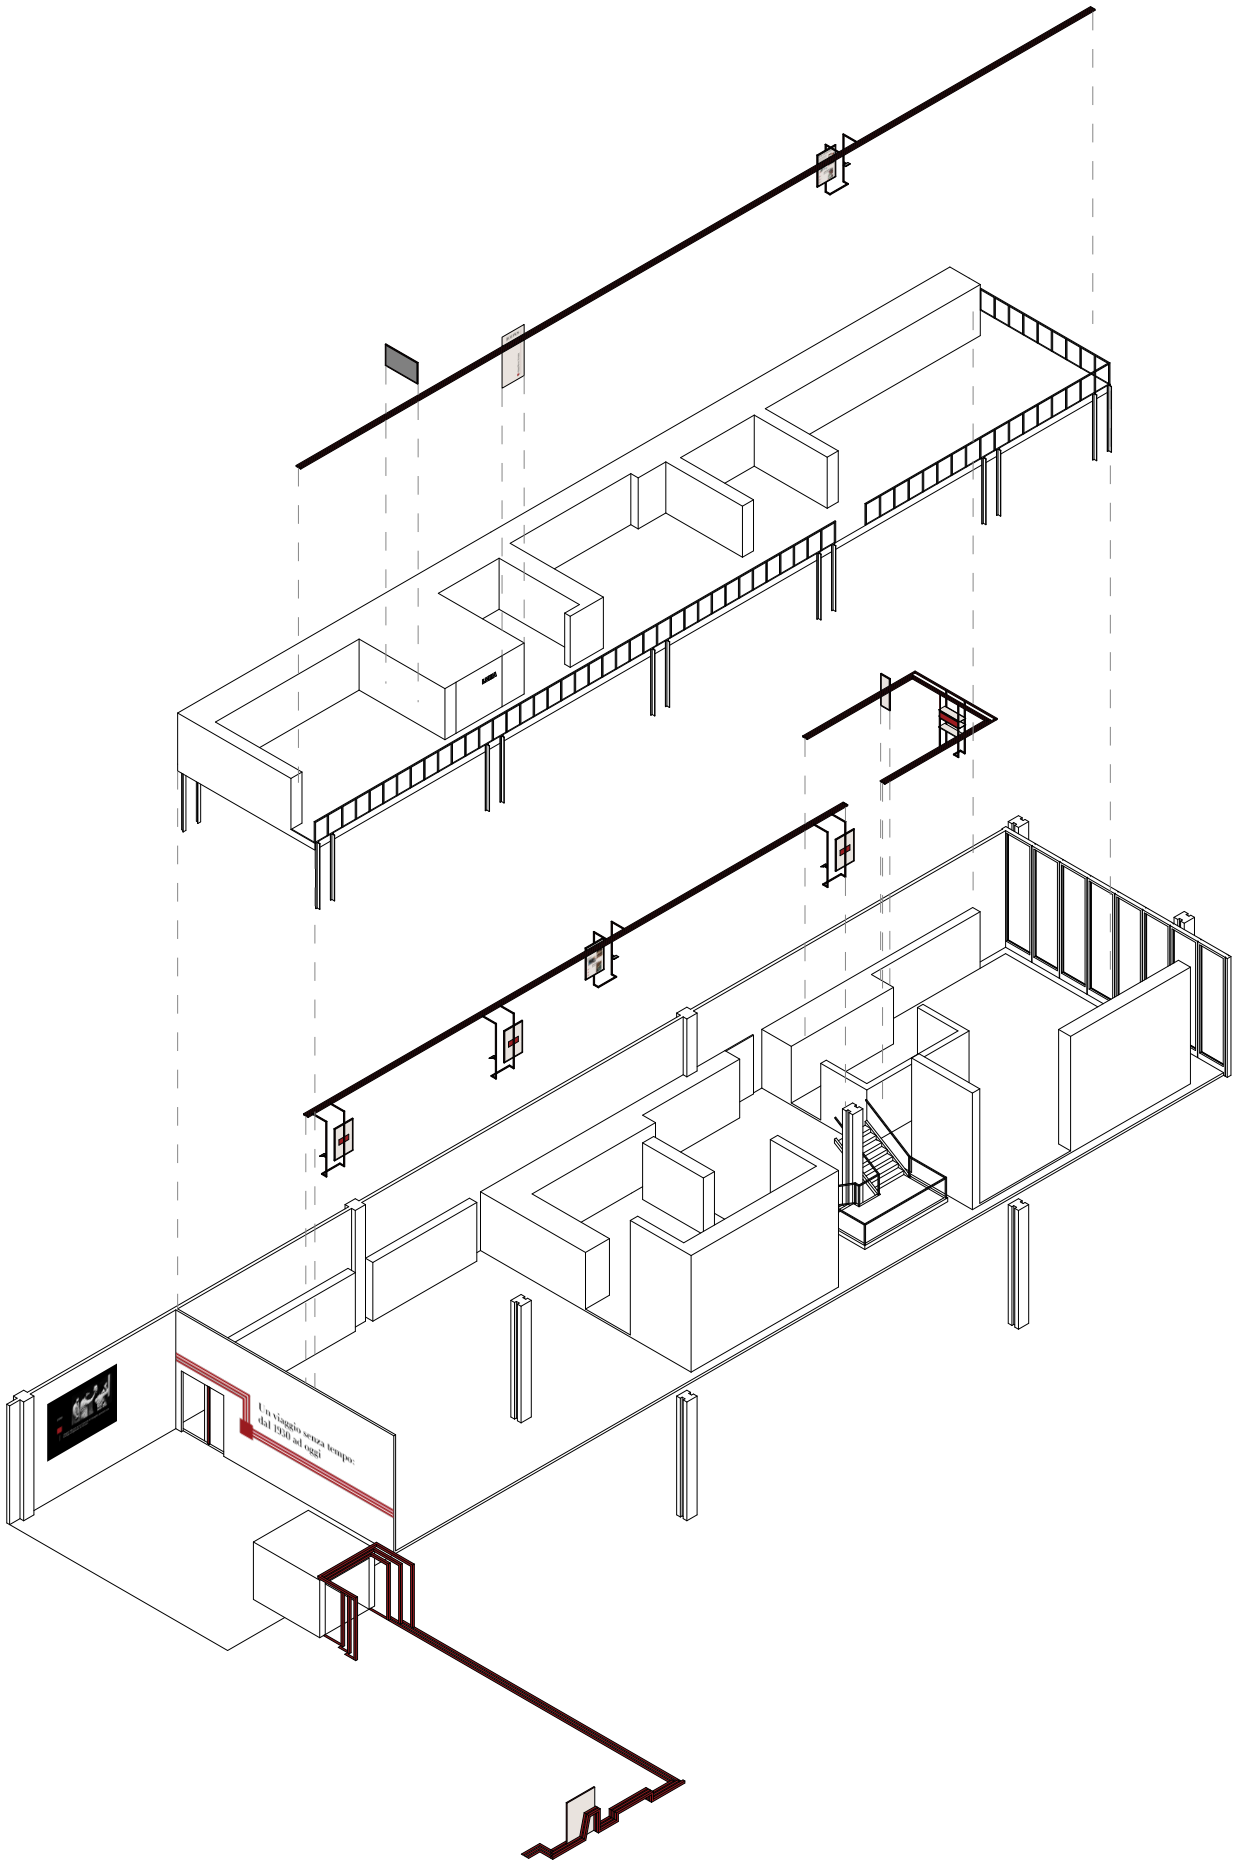

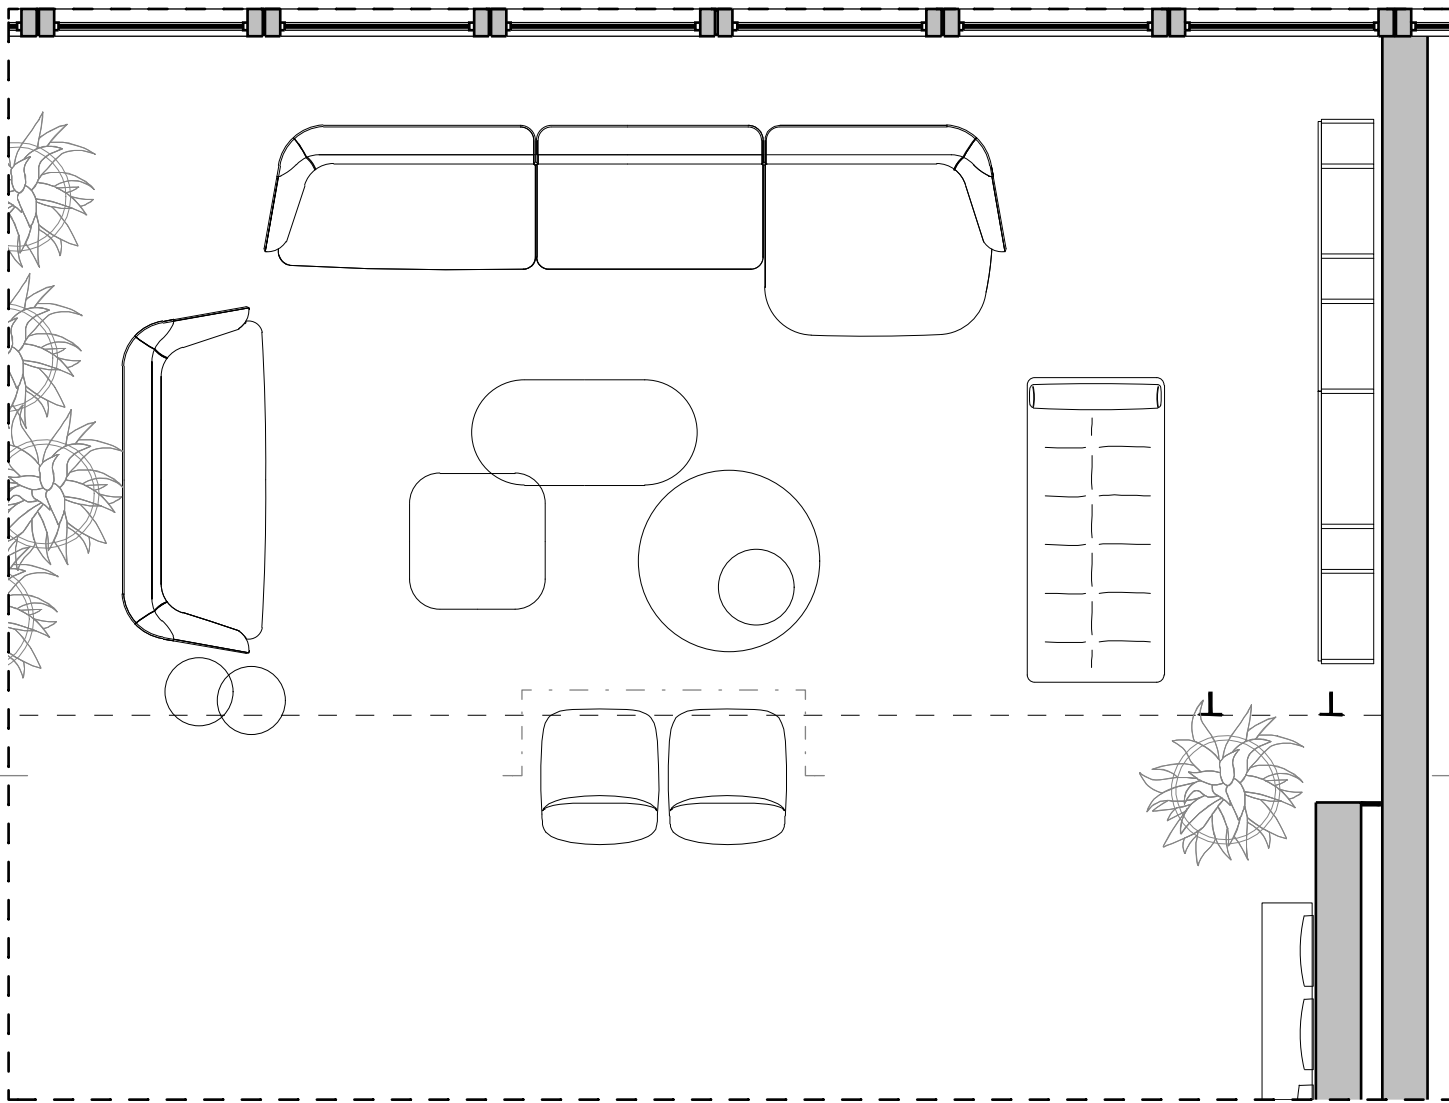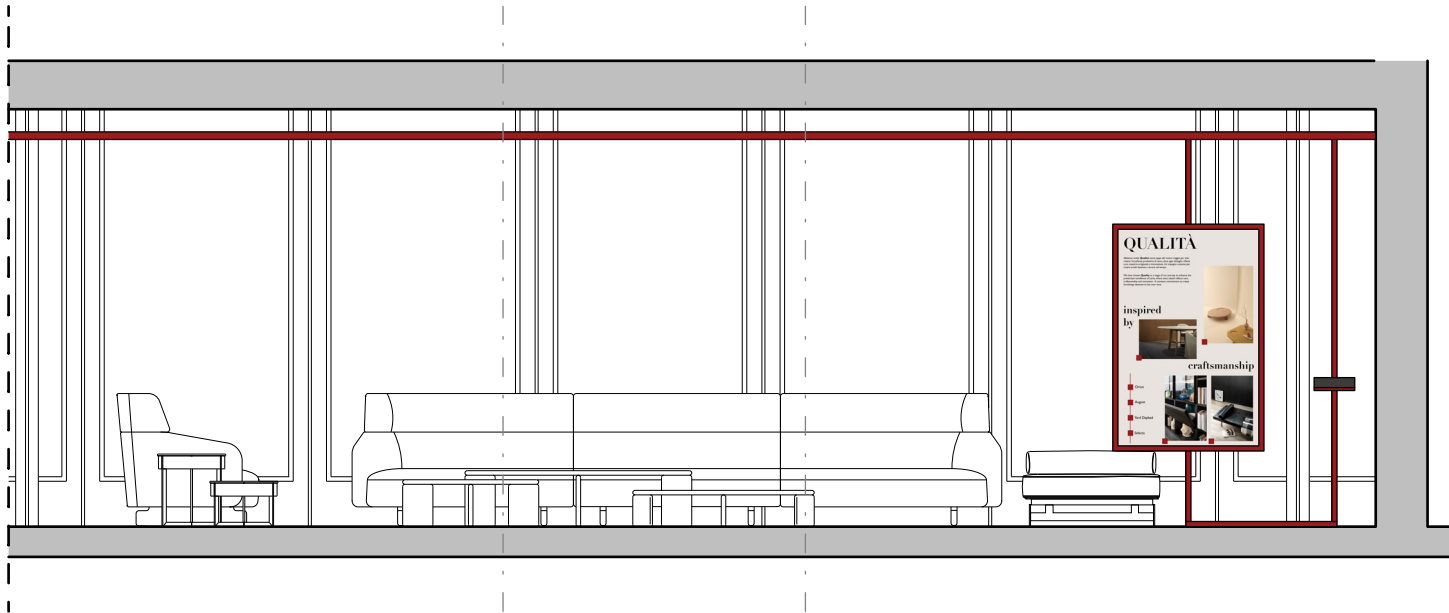


scala 1:50

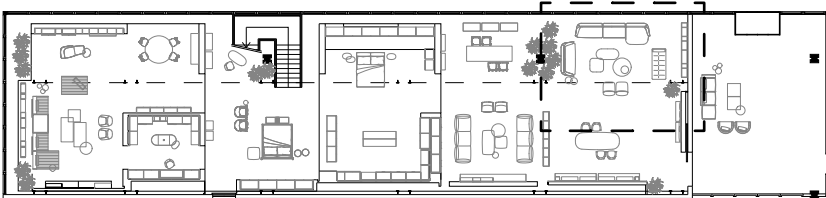

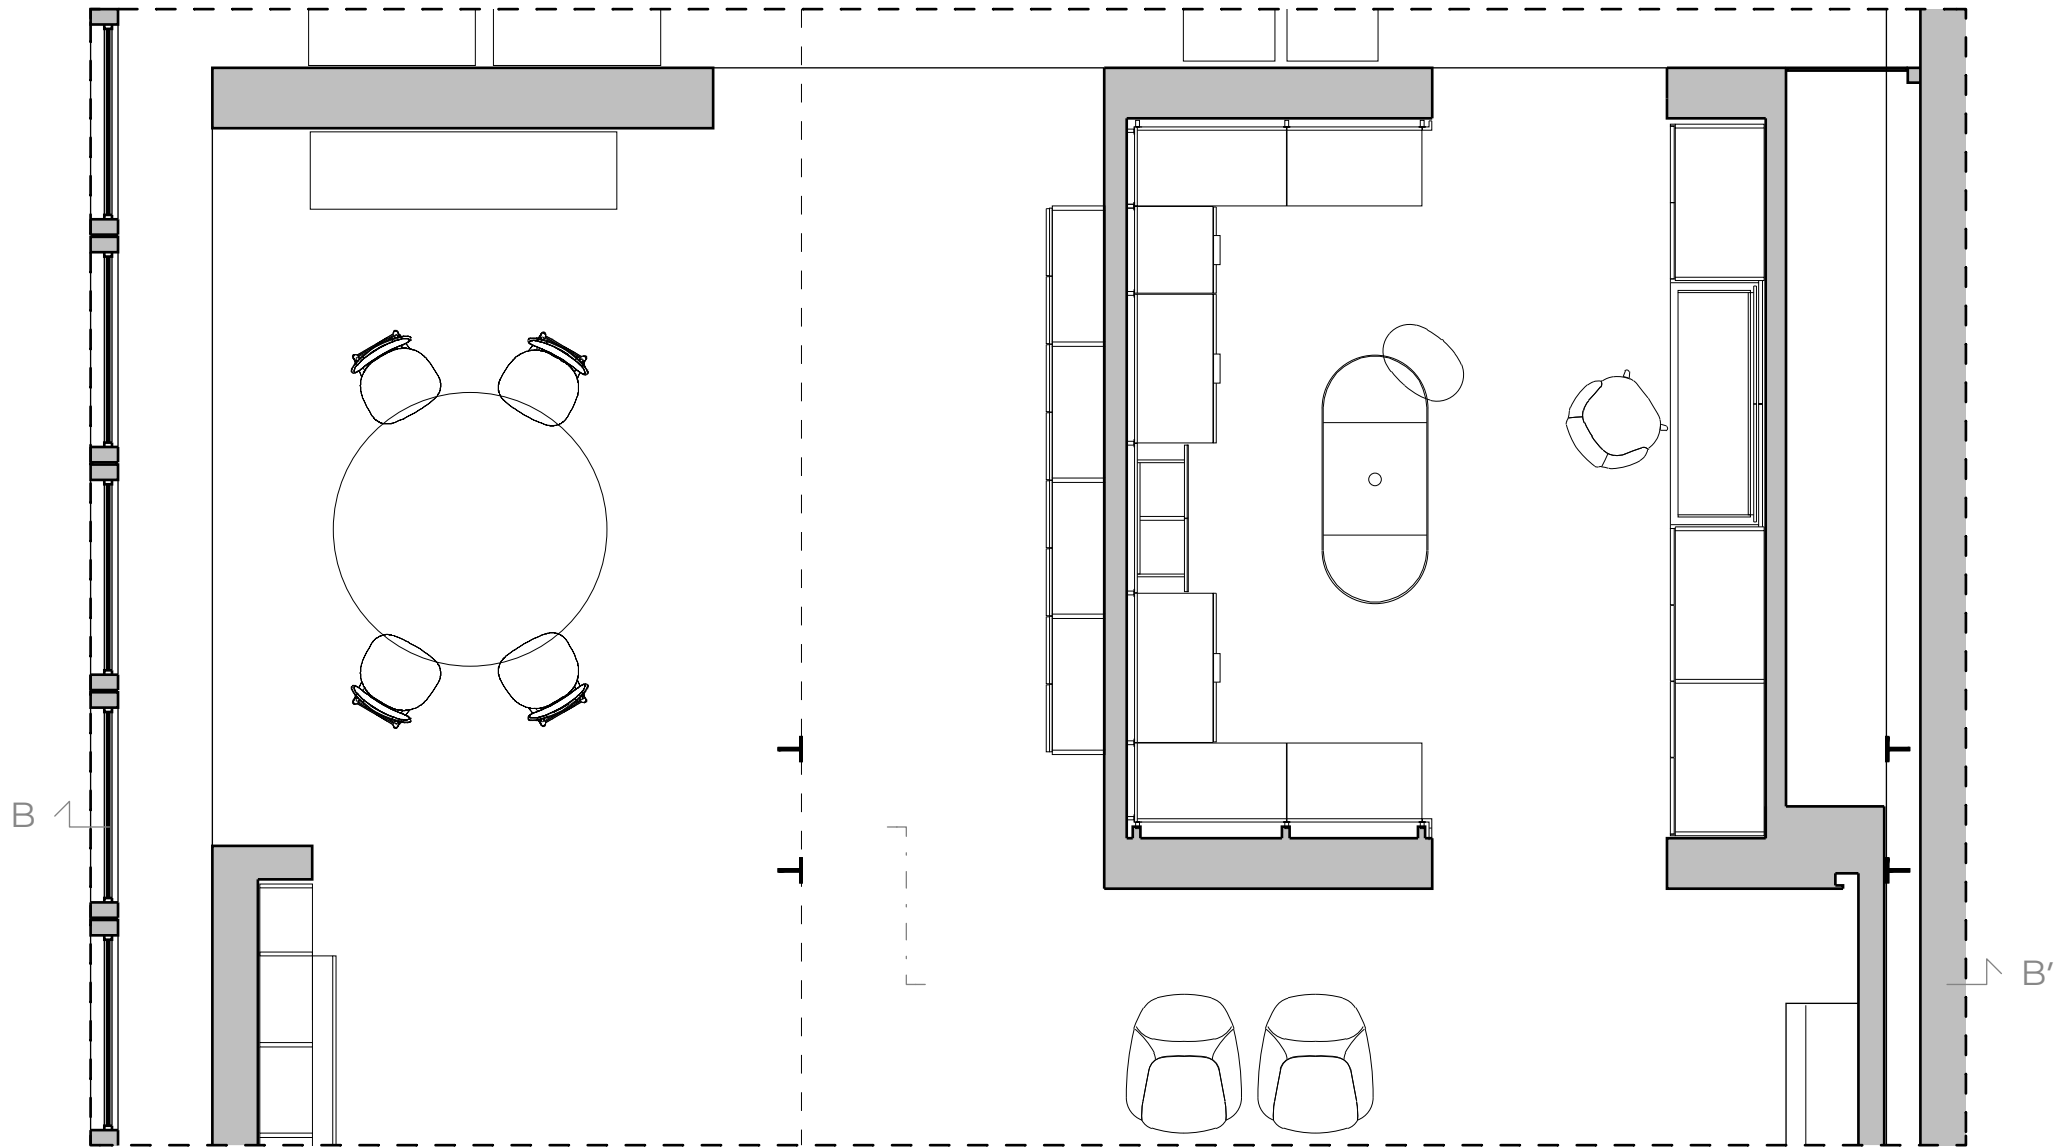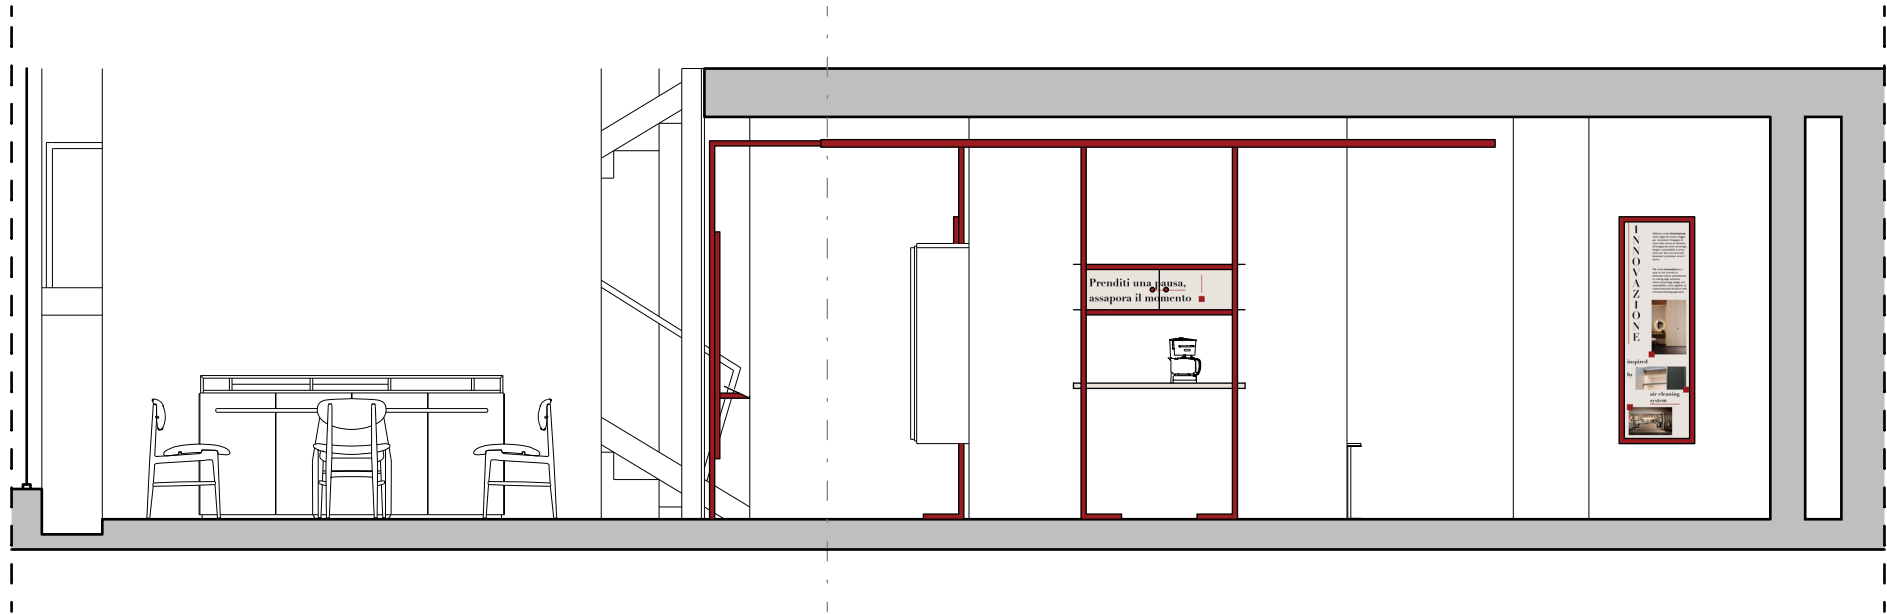


scala 1:50

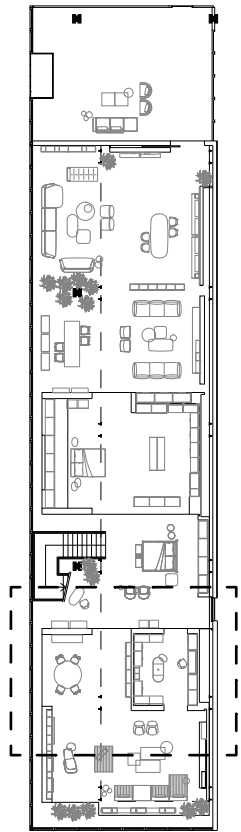






LUCE D'ACCENTO SCENOGRAFICA

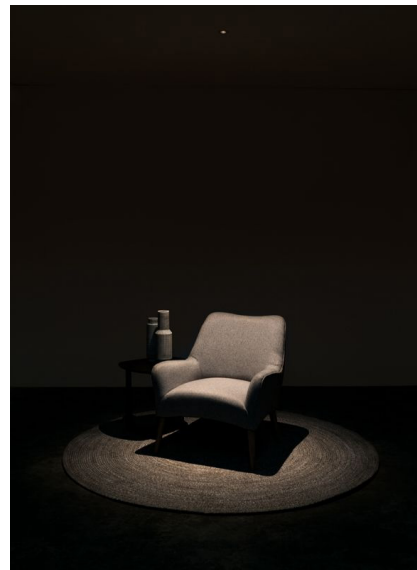


WAYFINDING LUMINOSO



GERARCHIA LUMINOSA

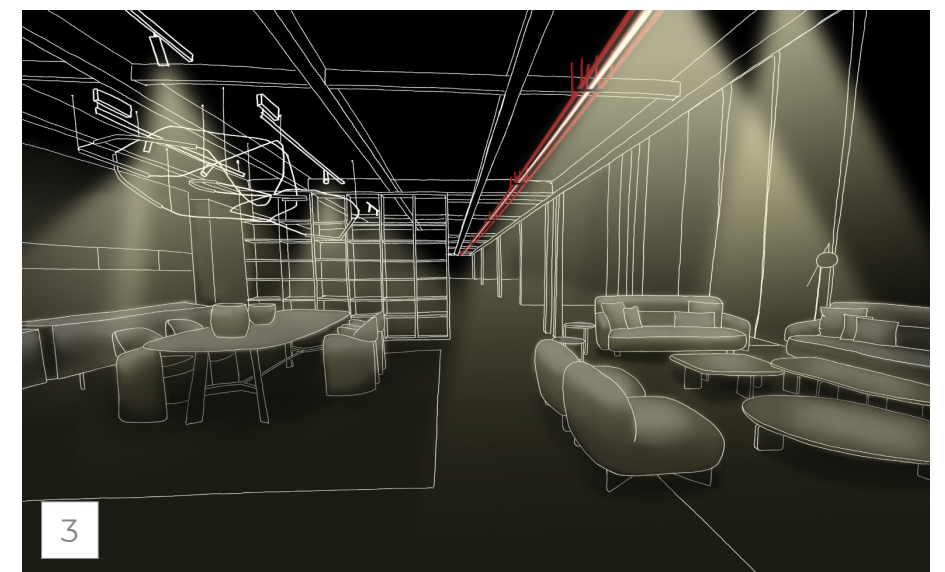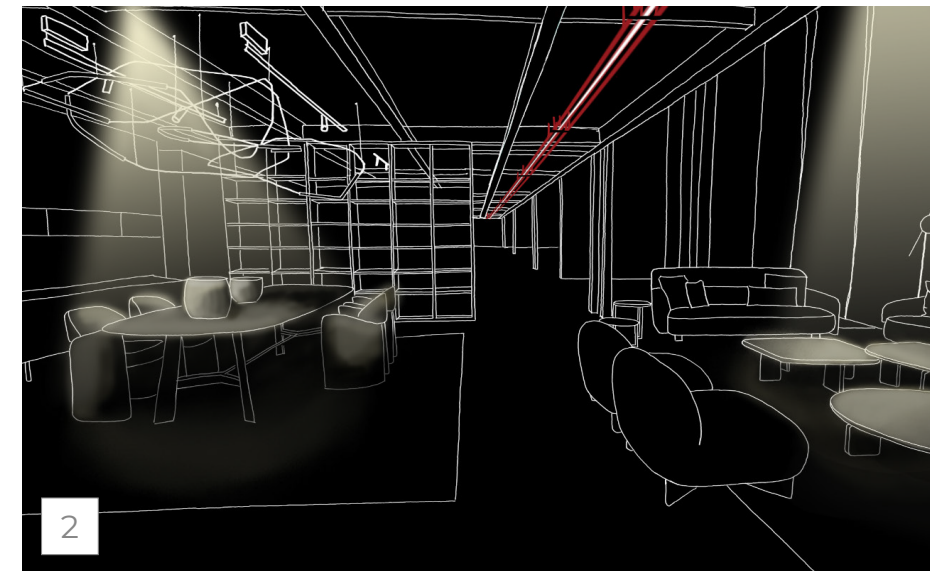
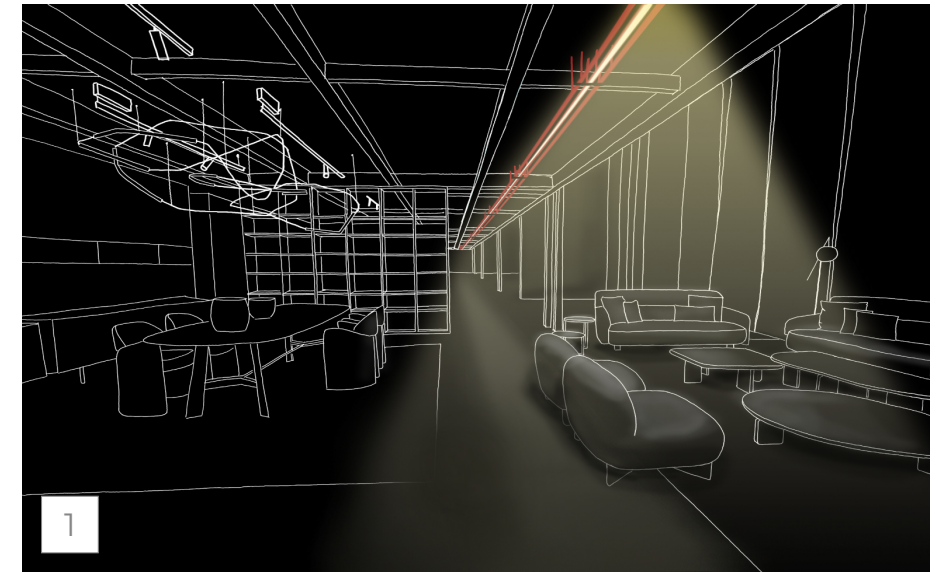


1. La striscia LED centrale funge da **fonte luminosa principale**, mentre gli altri apparecchi sono accesi con un'**intensità minima del 10%**.
Il controllo degli apparecchi avviene mediante il **sistema DALI**, gestibile da tablet.
2. Alcuni proiettori si accendono, proiettando **fasci di luce spot sugli arredi selezionati** tramite tablet; per alcuni proiettori vengono utilizzati dei **gobos** al fine di ottenere la medesima apertura di fascio luminoso.
3. Tutti i proiettori rimanenti aumentano progressivamente la loro intensità fino al massimo, garantendo un'**illuminazione generale uniforme e completa** dell'ambiente.

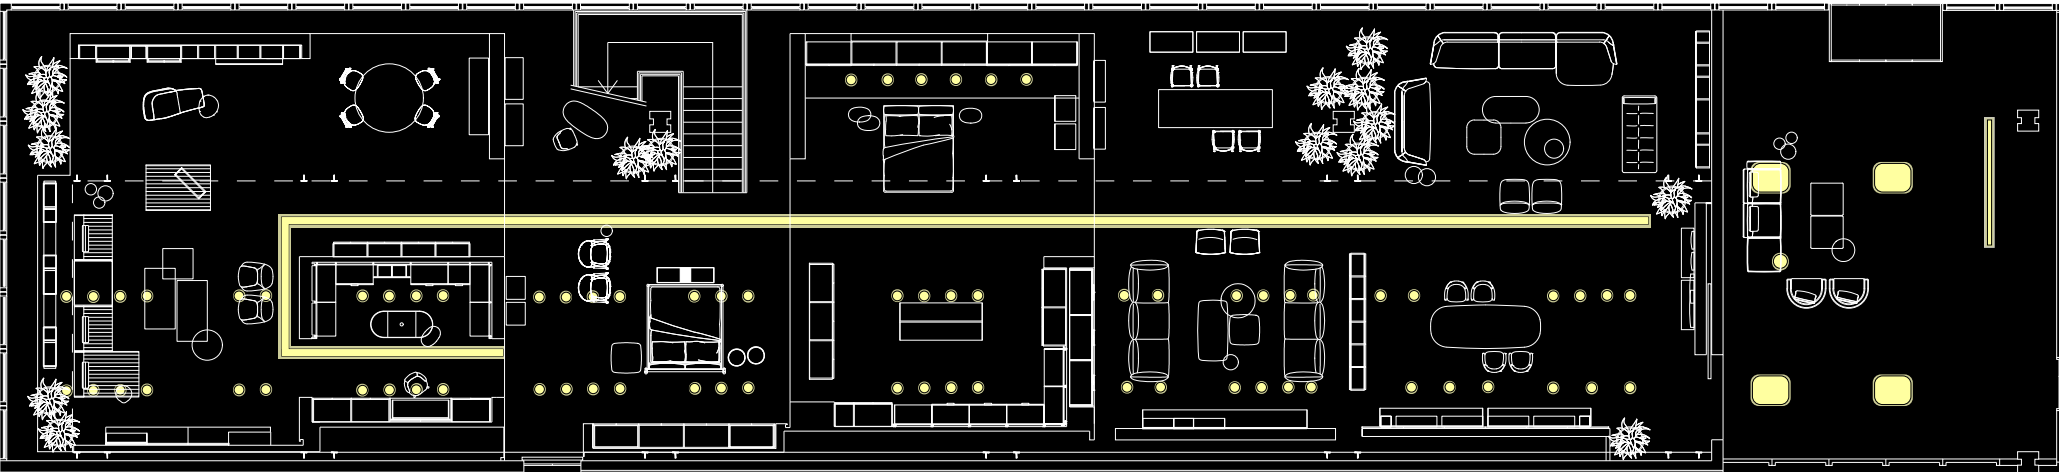

Pianta I livello

Gobos

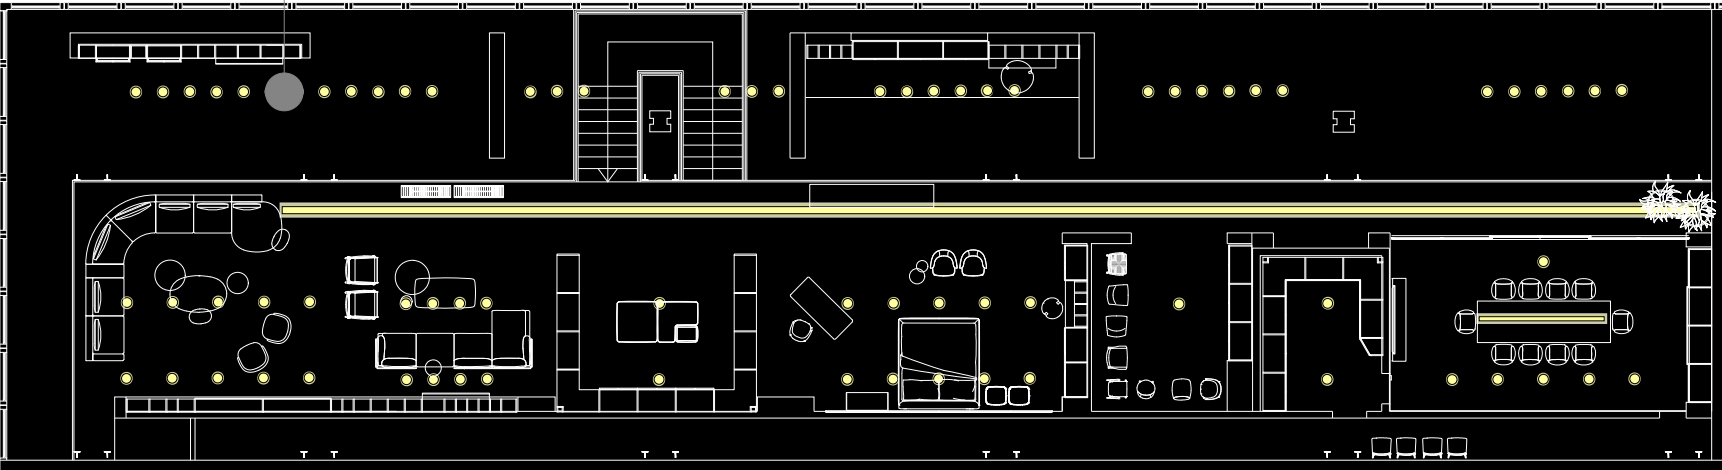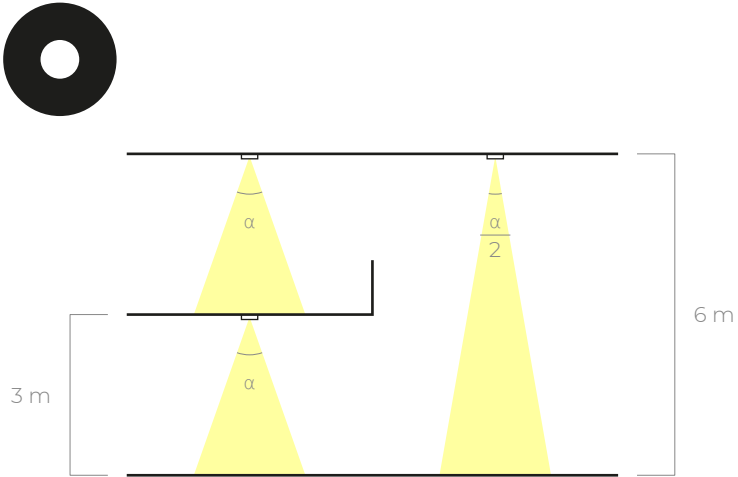


Pianta II livello


scala 1:200




Profilati 10x10 cm (sp. 1 mm) saldati tra loro
e chiusi alle estremità con delle piastrene
Azienda: Adriatica Metalli e Ferramenta

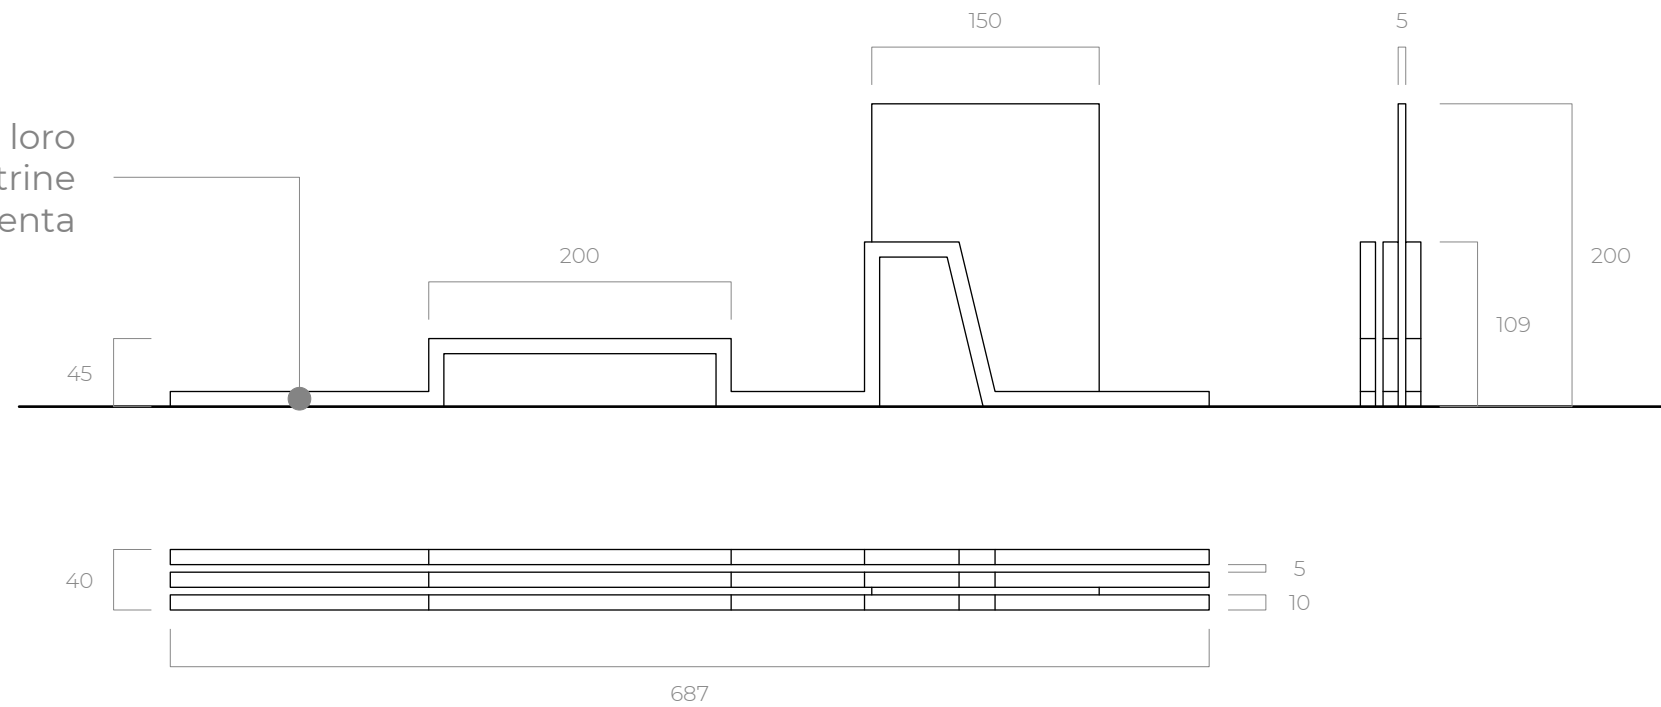


**Installazione area
esterna**
scala 1:50
unità di misura: cm

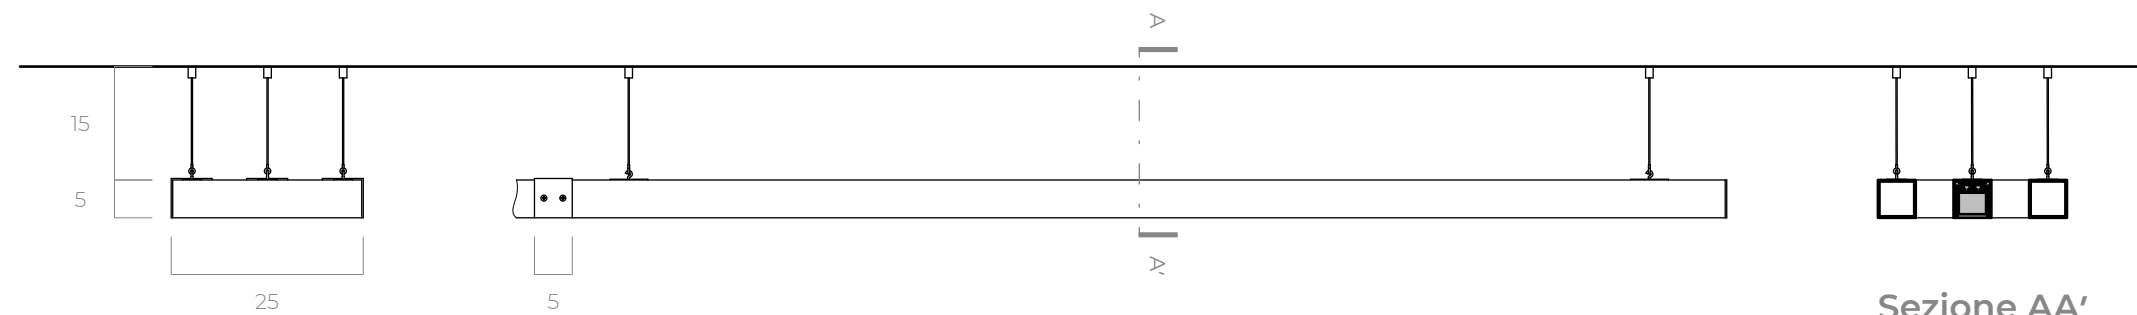

**Guide a soffitto
showroom**
scala 1:10
unità di misura: cm

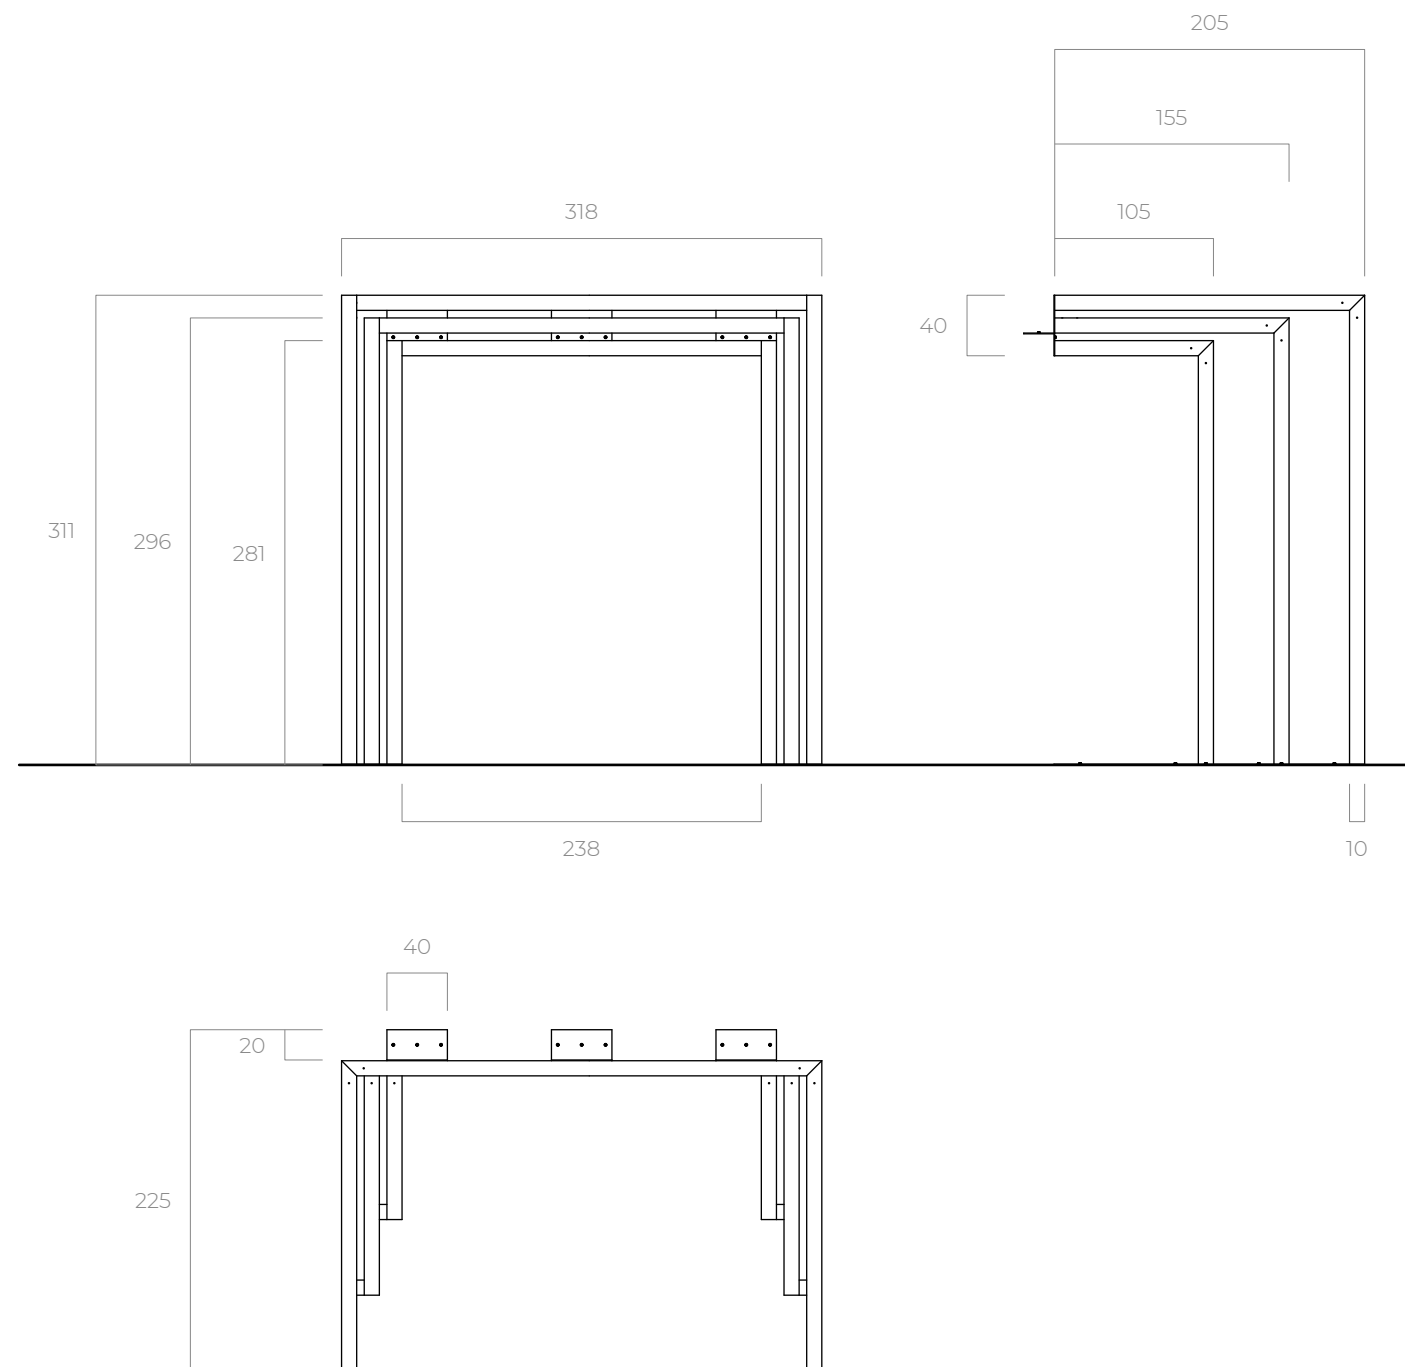

Portale d'ingresso
scala 1:50
unità di misura: cm


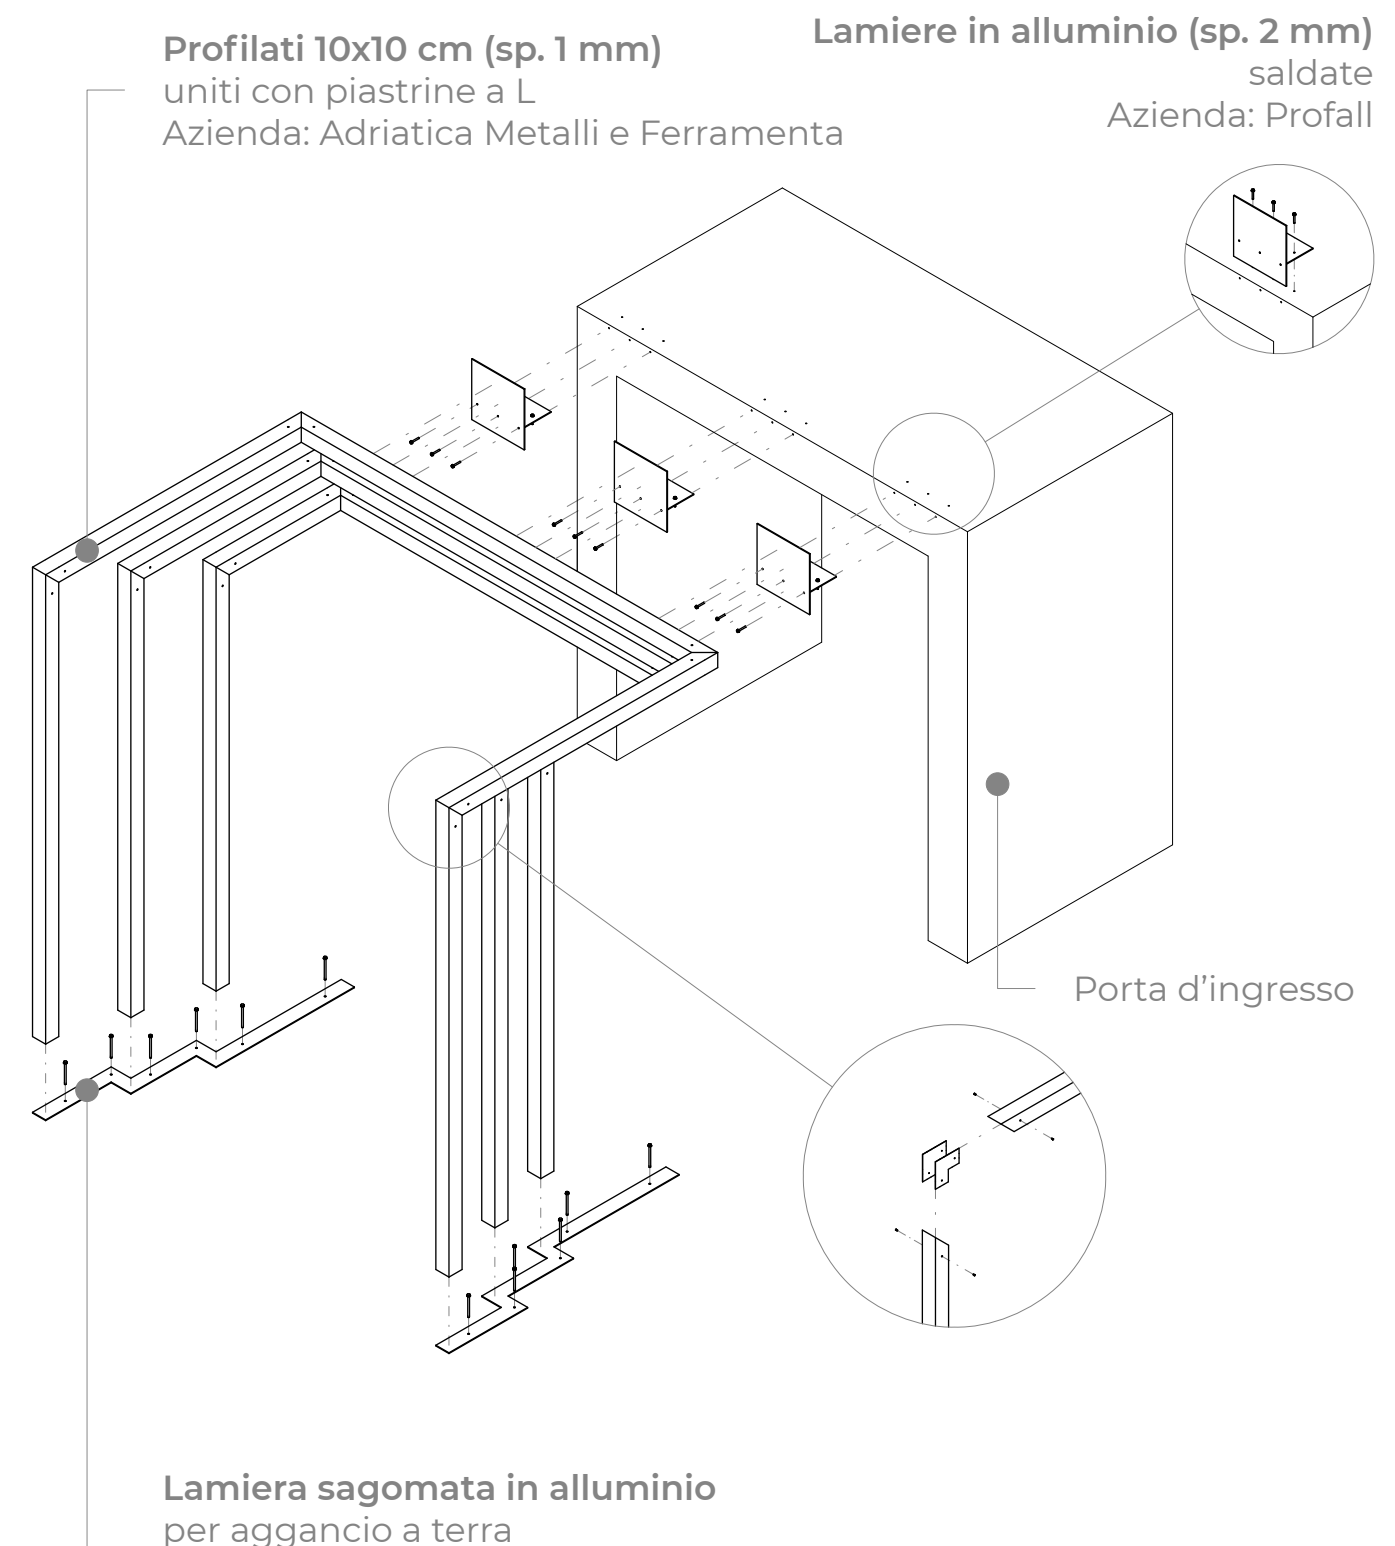


Profilati 10x10 cm (sp. 1 mm)
uniti con piastrelle a L
Azienda: Adriatica Metalli e Ferramenta


Lamiere in alluminio (sp. 2 mm)
saldate
Azienda: Profall

Lamiera sagomata in alluminio
per aggancio a terra
con viti per asfalto
Azienda: Profall


Esploso assonometrico
scala 1:50

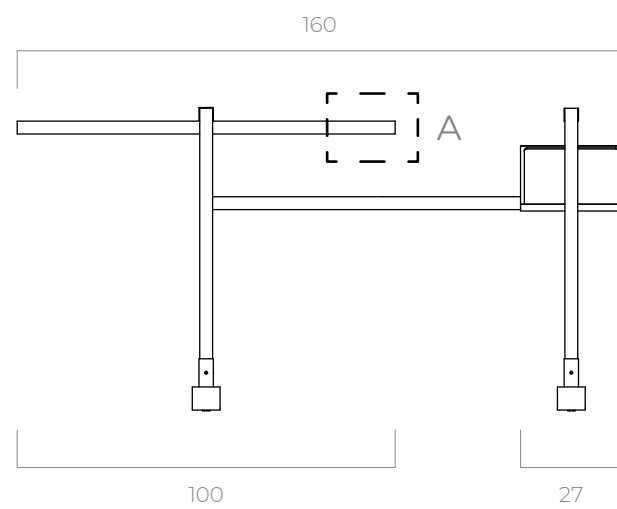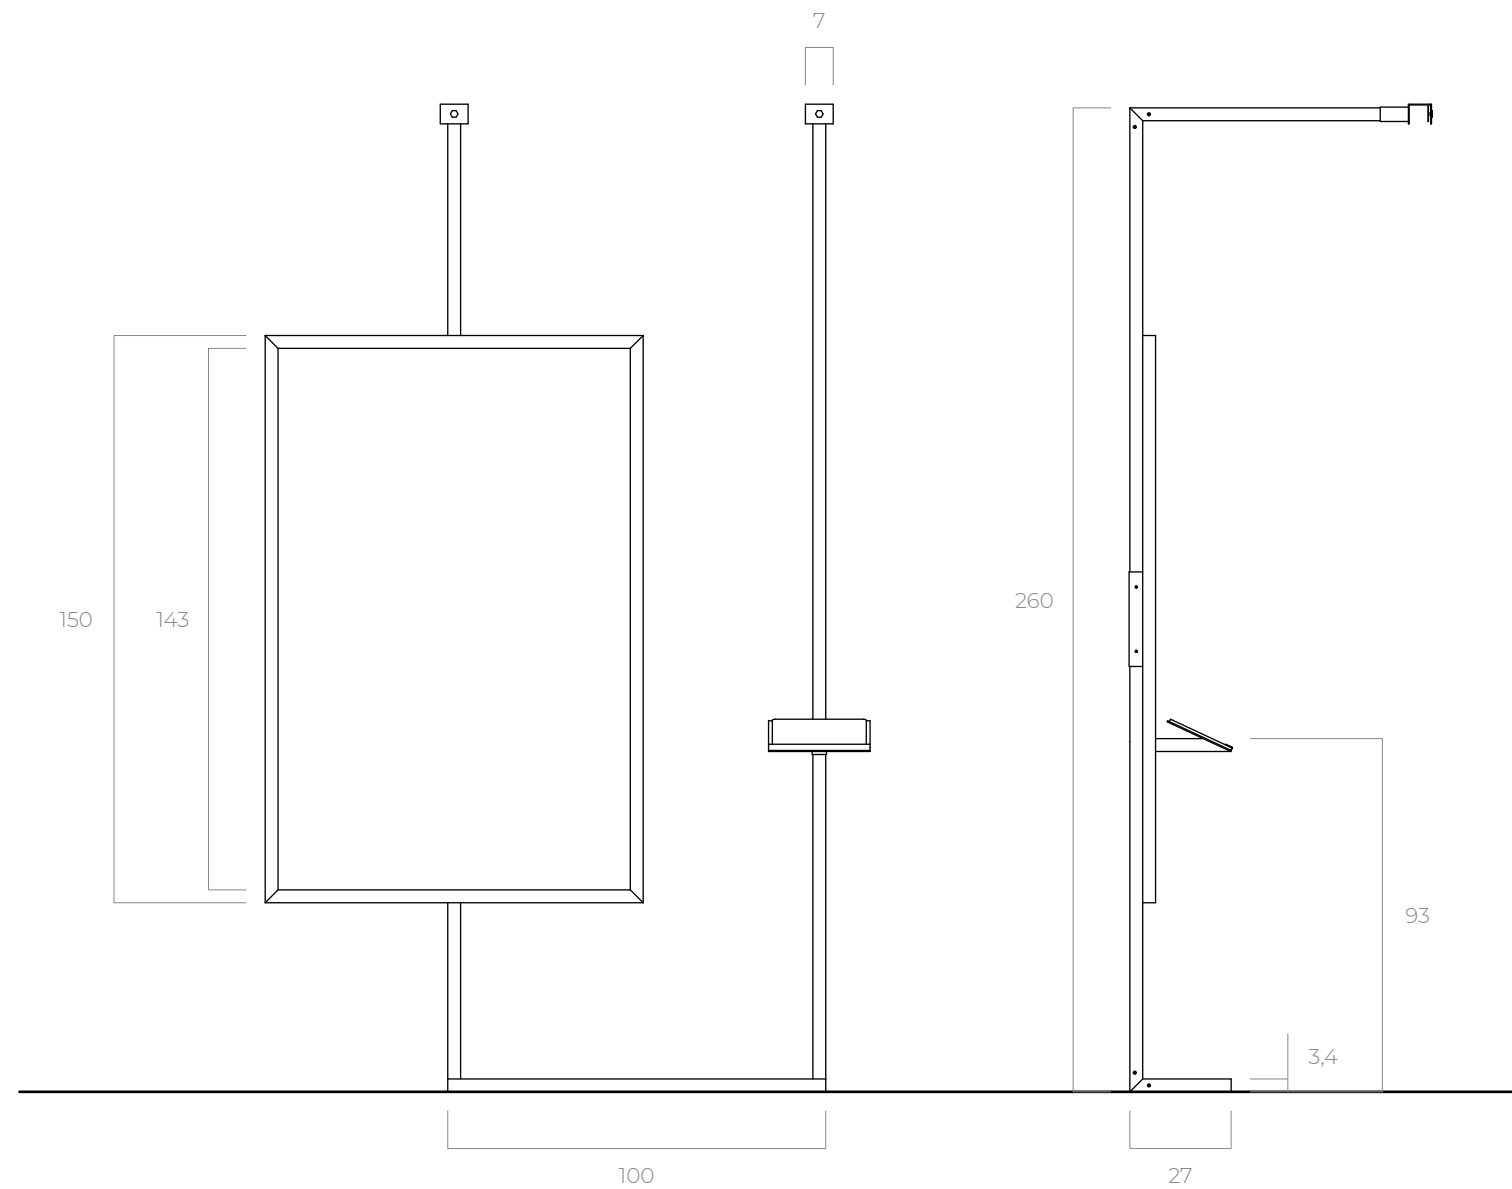


**Tabelloni fermate
showroom**
scala 1:20
unità di misura: cm

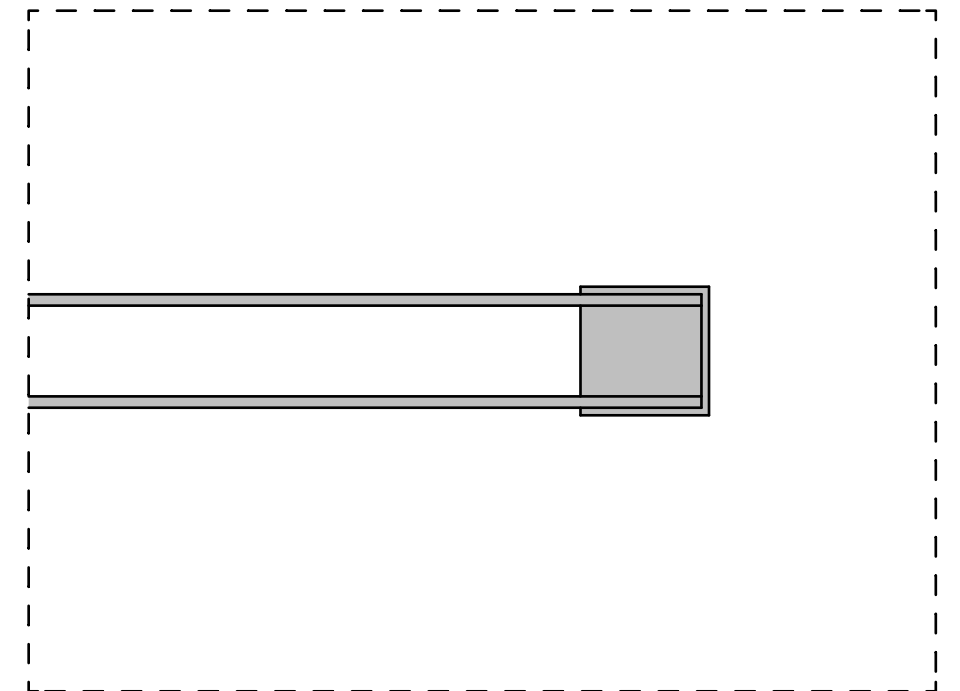


Sezione di dettaglio A
scala 1:2

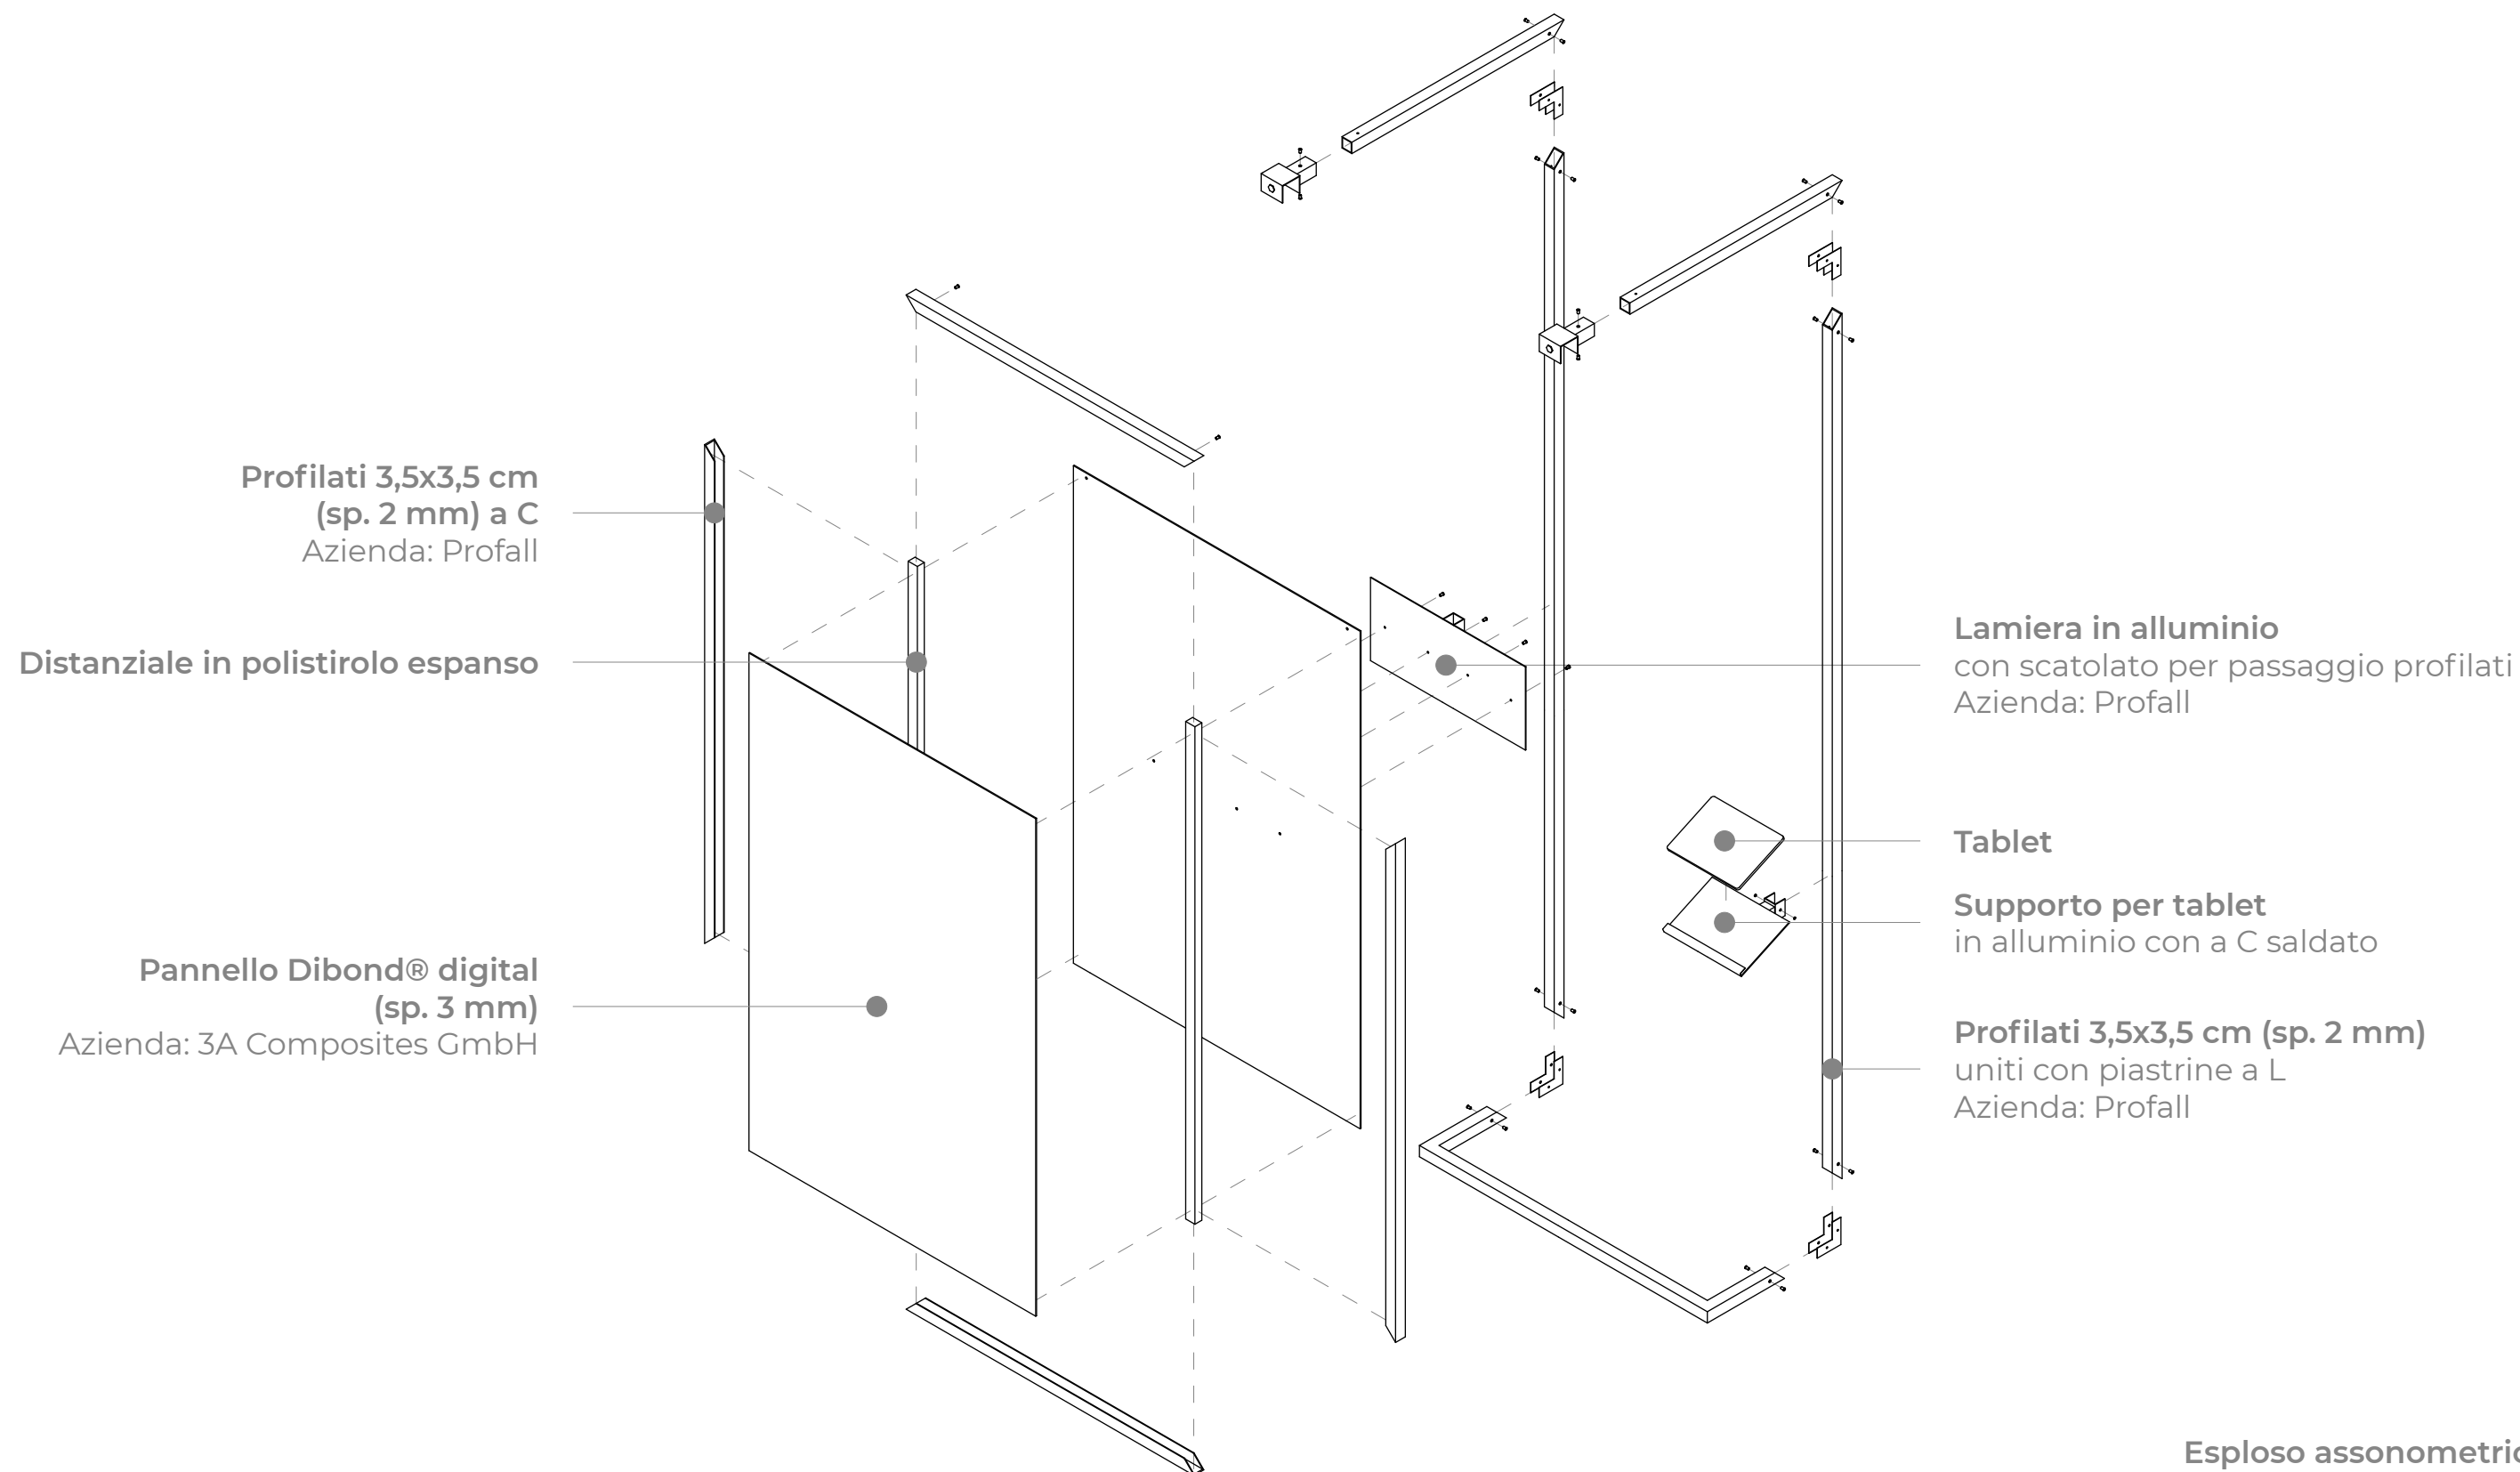

Esploso assonometrico
scala 1:20

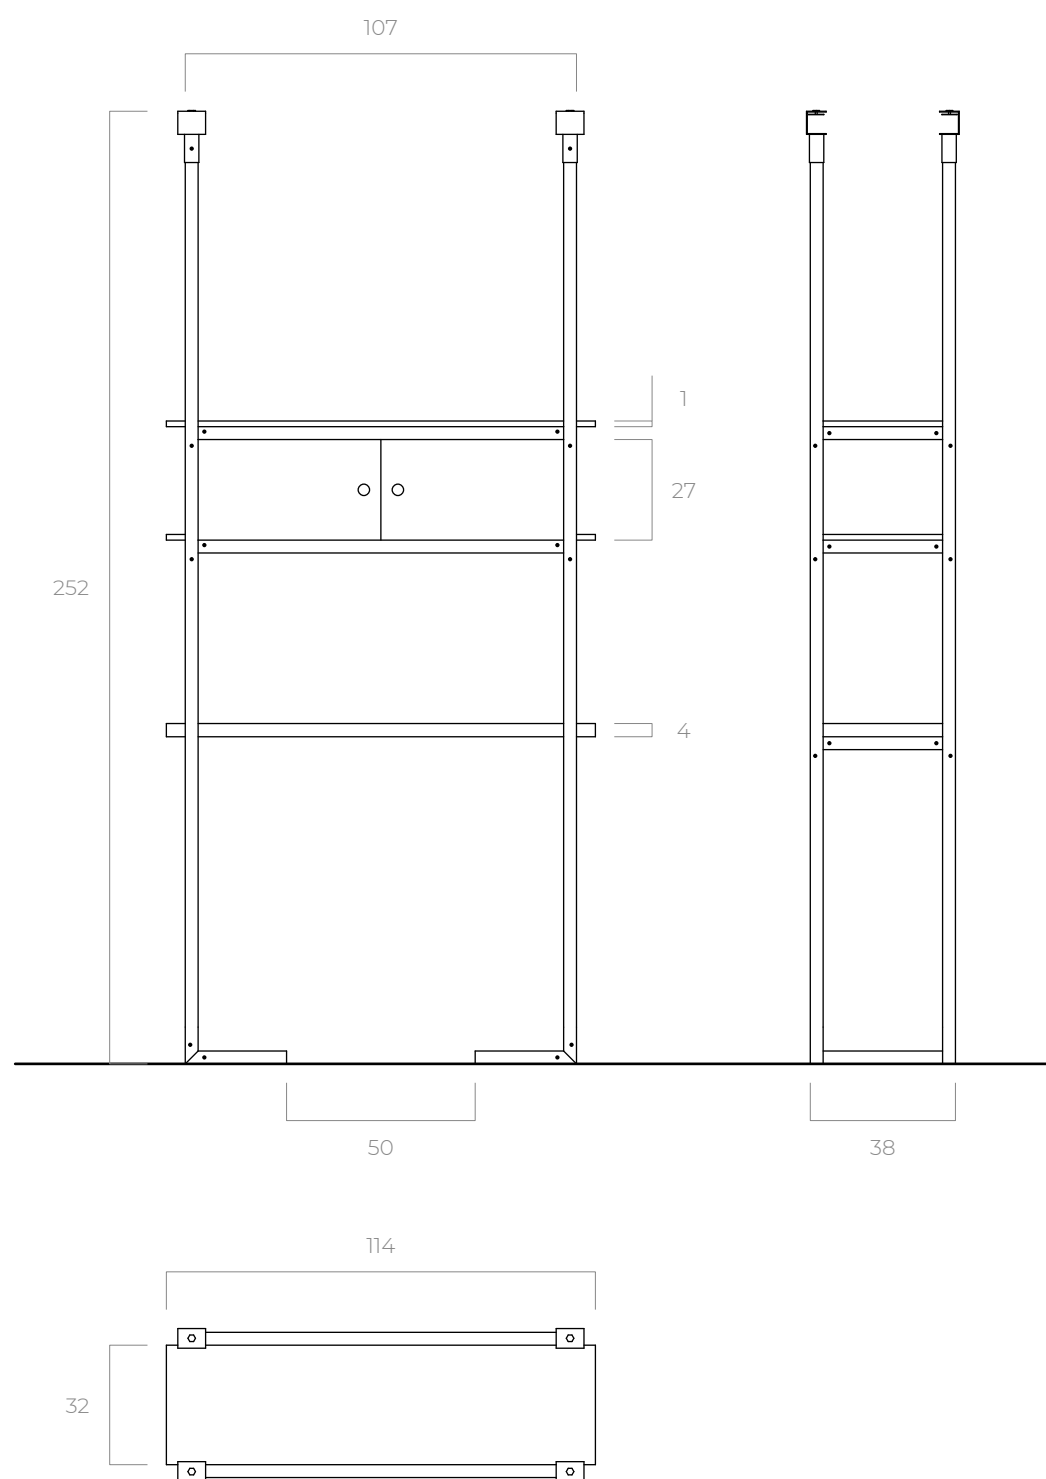

**Mobile fermata Relax
showroom**
scala 1:20
unità di misura: cm

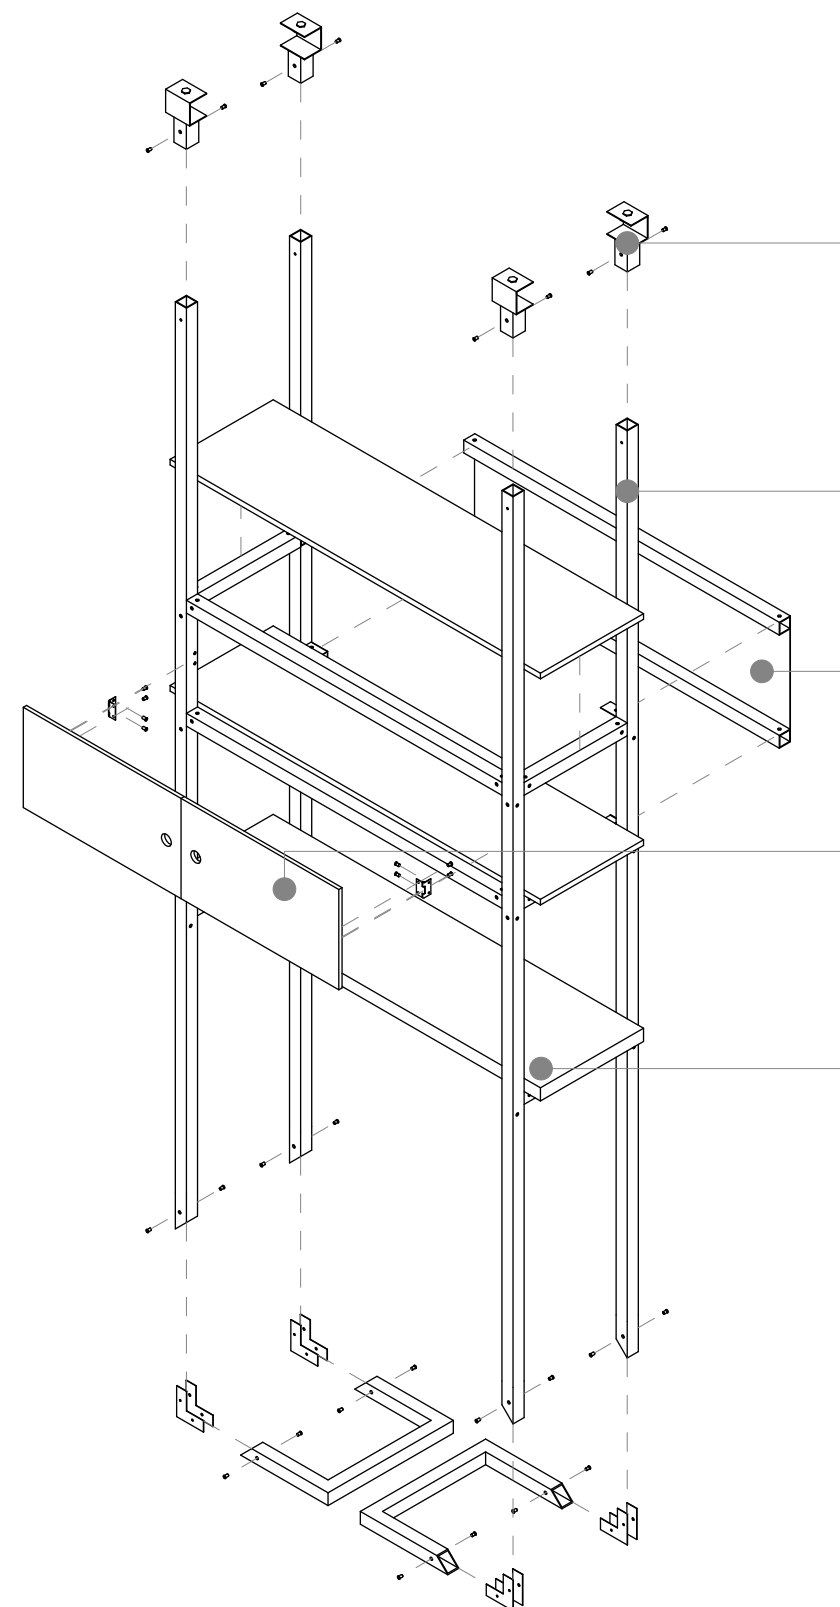

Ganci per guide a soffitto
con morsetti a C

Profilati 3,5x3,5 cm (sp. 2 mm)
uniti con piastrine a L
Azienda: Profall

Profilati 3,5x3,5 cm (sp. 2 mm)
saldati a lamiera in alluminio
Azienda: Profall

Ante in MDF (sp. 6 mm)
con pannello in Dibond®
digital applicato (sp. 3 mm)

Ripiani sistema Plain
di Francesco Rota
Azienda: Lema
[PROPOSTA NUOVA
FINITURA]

Esploso assonometrico
scala 1:20